


626.250.PB.012.000.000СБ

Перв. примен.				
Справ. №				
Подп. и дата				
Инв. № дудл.				
Взам. инв. №				
Подп. и дата				
Инв. № подл.				

Поз.	Обозначение	Наименование	Кол-во.	масса
1	010.4.6.001.000	Контактная группа	1	0.89
2	626.250.PB.012.001.000	Корпус КОМ	1	14.14
3	626.250.PB.012.000.001	Шина	1	0.13
4	626.250.PB.012.000.002	Шина	1	0.13
5	626.250.PB.012.000.003	Шина	1	0.09
6	626.250.PB.012.000.004	Шина N	1	0.19
7	626.250.PB.012.000.005	Шина PE	1	0.12
8	626.250.PB.012.000.006	Расширитель	1	0.02
9	626.250.PB.012.000.007	Расширитель	2	0.02
10	11538.000.036 кондуктор	Планка крепления	1	0.02
11		Шинный изолятор SM 25	2	0,02
12		Автоматический выключатель MNX250L_M_H_3P	1	3917.01
13		Ручка TFH_250	1	1098.27
14		Болт DIN 6921-M6x16-8.8	4	
15		Болт DIN 6921-M6x20-8.8	8	
16		Болт DIN 933-M10x35-8.8	10	
17		Болт DIN 933-M12x30-8.8	5	
18		Гайка DIN934-M10-8.8	10	0.02
19		Гайка DIN 985-M6-8.8	8	
20		Шайба DIN 125-6-Zn	8	
21		Шайба DIN 125-10-Zn	20	
22		Шайба DIN 127-10-Zn	10	
23		Гайка DIN934-M12-8.8	5	0.02
24		Шайба DIN 125-12-Zn	10	
25		Шайба DIN 127-12-Zn	5	
26		Наклейка "А" 20мм	1	0.00
27		Наклейка "В" 20мм	1	0.00
28		Наклейка "С" 20мм	1	0.00
29		Наклейка "Знак N" 20мм	1	0.00
30		Наклейка "Знак заземления" 20мм	1	0.00
31		Трубка термоусаживаемая ТУТ-20 10 зеленый 150мм	1	0,09
32		Трубка термоусаживаемая ТУТ-20 10 синий 245мм	1	0,19
33		Трубка термоусаживаемая ТУТ-20 10 жз 170мм	1	0,12

Дверь условно не показана


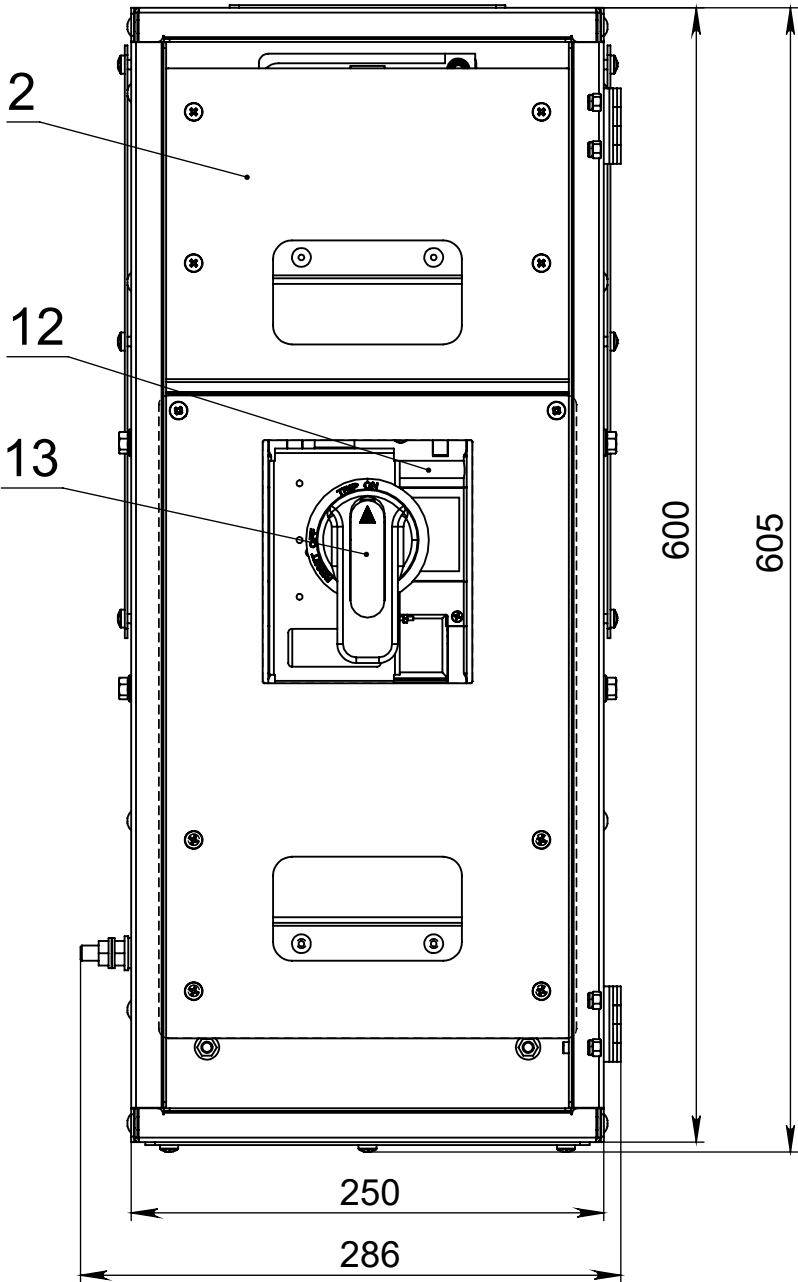


- 1. Размеры для справок.
- 2. Общие допуски по ГОСТ 30893.2-тК.
- 3. Знак электрической безопасности нанести на фальш-панель. Допускается ввиде наклейки. На шины поз. 3, 4, 5, 6, 7 наклеить наклейки фазировки шин поз. 26, 27, 28, 29, 30 согласно фазировки в 1С (ТЗ).
- 4. На шины поз. 4, 6, 7 надеть термоусаживаемую трубку ТУТ 20/10 поз. 31, 32, 33. Размеры указаны в чертежах на данные шины.

					626.250.РВ.012.000.000СБ				
					КОМ 250А с ручкой Сборочный чертеж				
Изм.	Лист	№ докум.	Подп.	Дата					
Разраб.		Михайлова		18.08.2026					
Пров.		Стожаров		18.08.2026					
Т. контр.		Безруков		18.08.2026					
Н. контр.		Стожаров		18.08.2026					
Утв.		Банников П		18.08.2026					

Инв. № подл.	Подп. и дата	Взам. инв. №	Инв. № дудл.	Подп. и дата

626.250.PB.012.000.000СБ

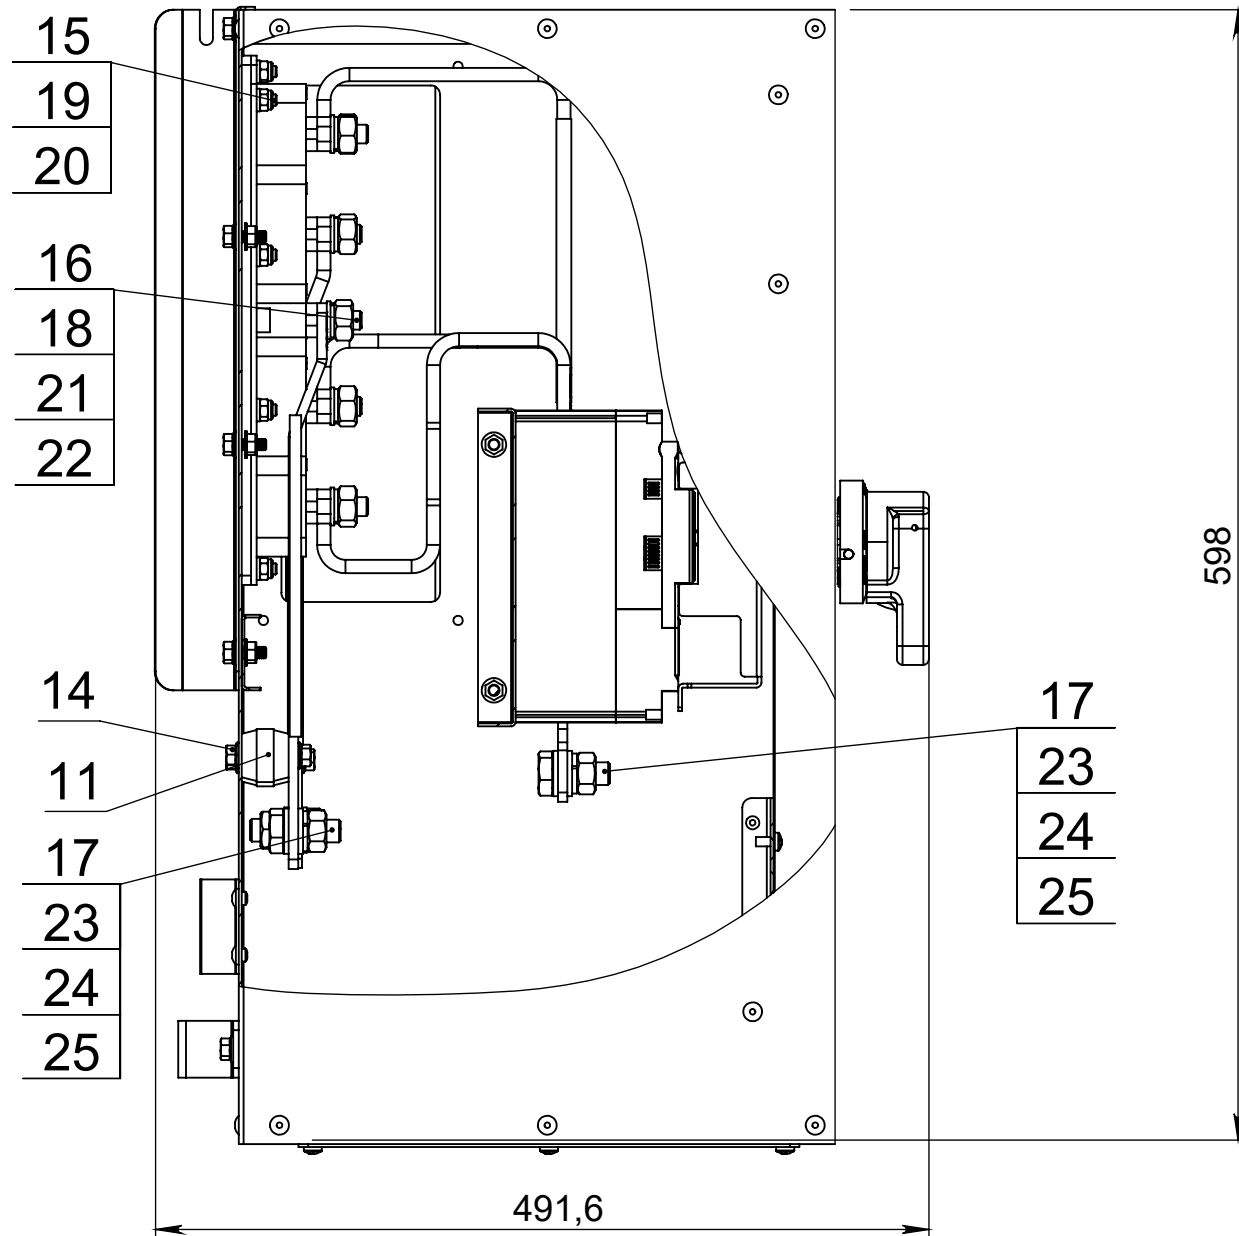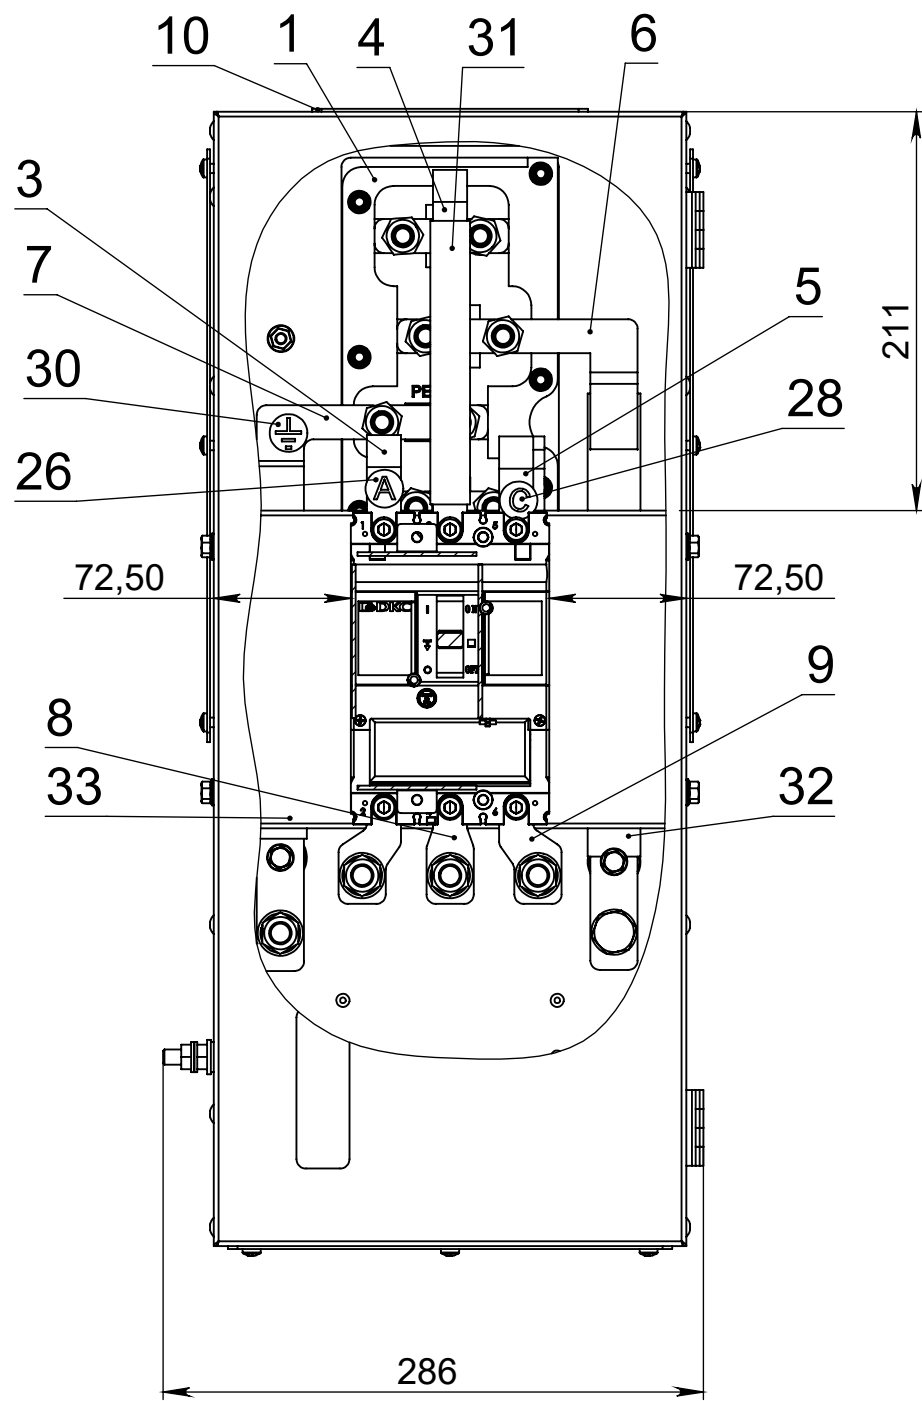

Изм.	Лист	№ докум.	Подп.	Дата

626.250.PB.012.000.000СБ

Лист
2