


Фрагмент плана расположения щитового оборудования в осях Б / 8
отм. -5,600 М(1:50)

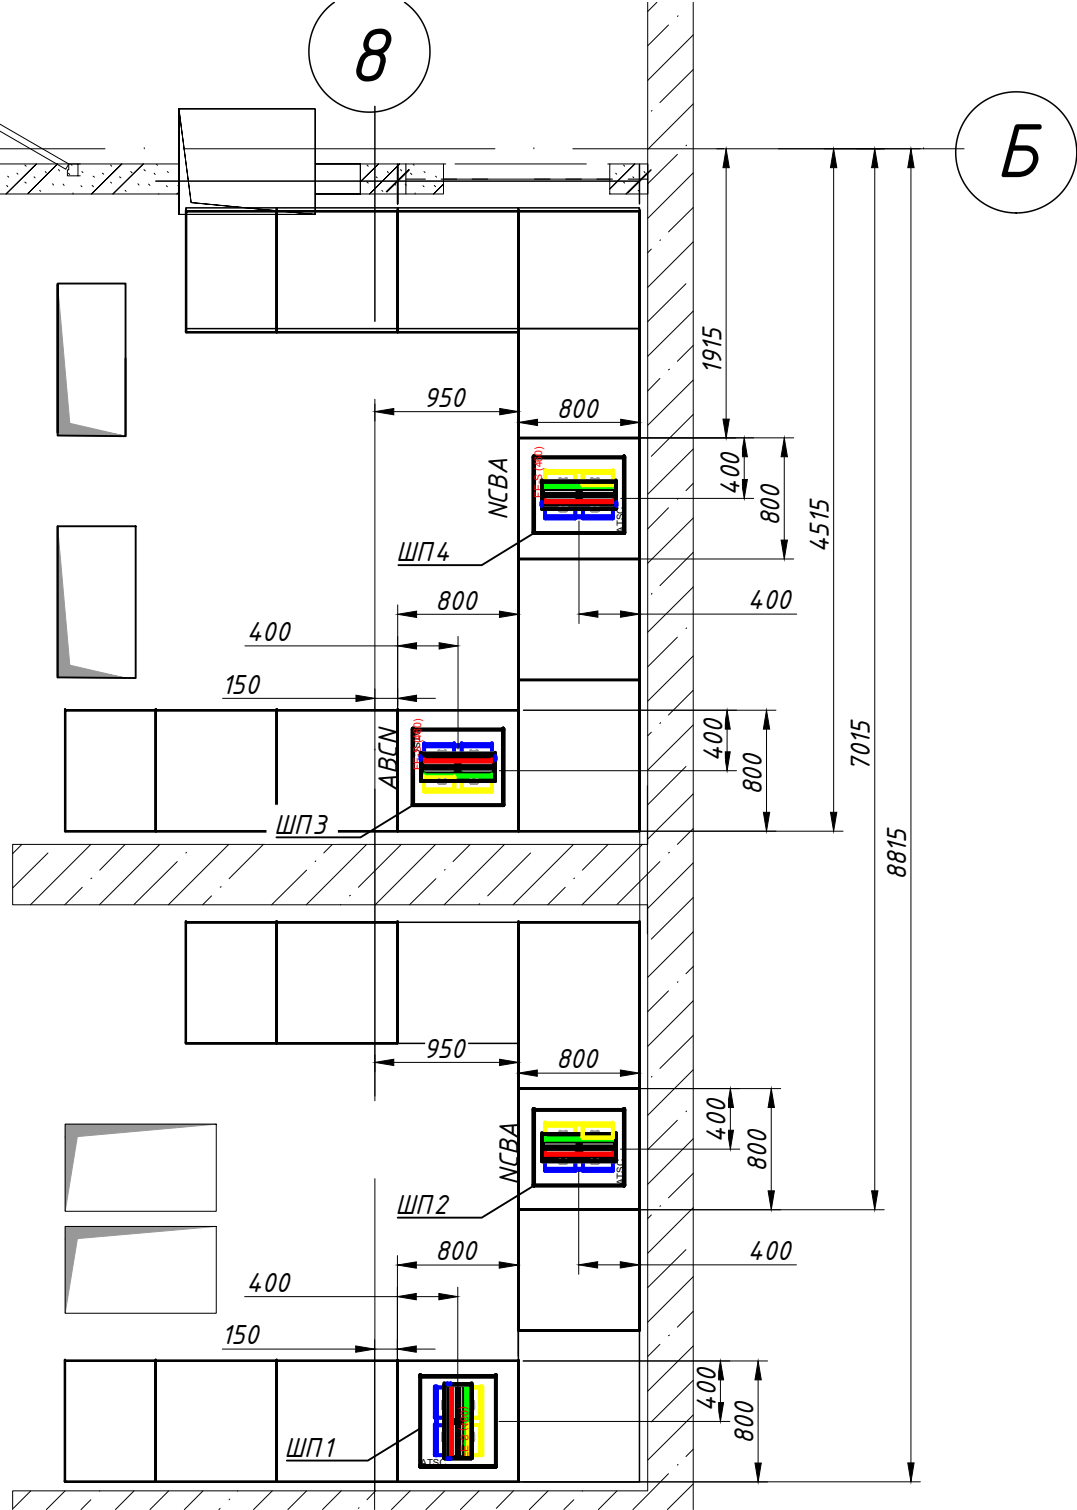

- Условные обозначения
- ШП1 – обозначение линии шинпровода KLM-S-40-AI-55-4-V3;
 - ШП2 – обозначение линии шинпровода KLM-S-40-AI-55-4-V3;
 - ШП3 – обозначение линии шинпровода KLM-S-40-AI-55-4-V3;
 - ШП4 – обозначение линии шинпровода KLM-S-40-AI-55-4-V3;
- Примечания
- Порядок сборки линий шинпровода определяется последовательностью элементов в сборочной таблице;
 - Монтаж шинпроводной линии осуществлять в соответствии с инструкцией по монтажу;
 - Элементы крепежа шинпровода следует размещать таким образом, чтобы стыковочные элементы не несли механической нагрузки;
 - Высотные отметки указаны от нижней грани шинпровода;
 - Указанные размеры ориентировочные. Габариты шинпровода (ВхШ): KLM-S-40-AI-55-4-V3 – 488х140мм
 - Высотные отметки указаны в абсолютных координатах;

Приложение № 9 к Договору поставки
№ МК2507/18 от 08.07.2025


СОГЛАСОВАНО
ООО "МК Инжиниринг"
Генеральный директор
_____/Карпова М. И./

М.П.

СОГЛАСОВАНО
ТОО "Айтек"
_____/Виноградов К. П./


М.П.

Фрагмент плана прокладки шинпровода в осях Б / 8
отм. -5,600

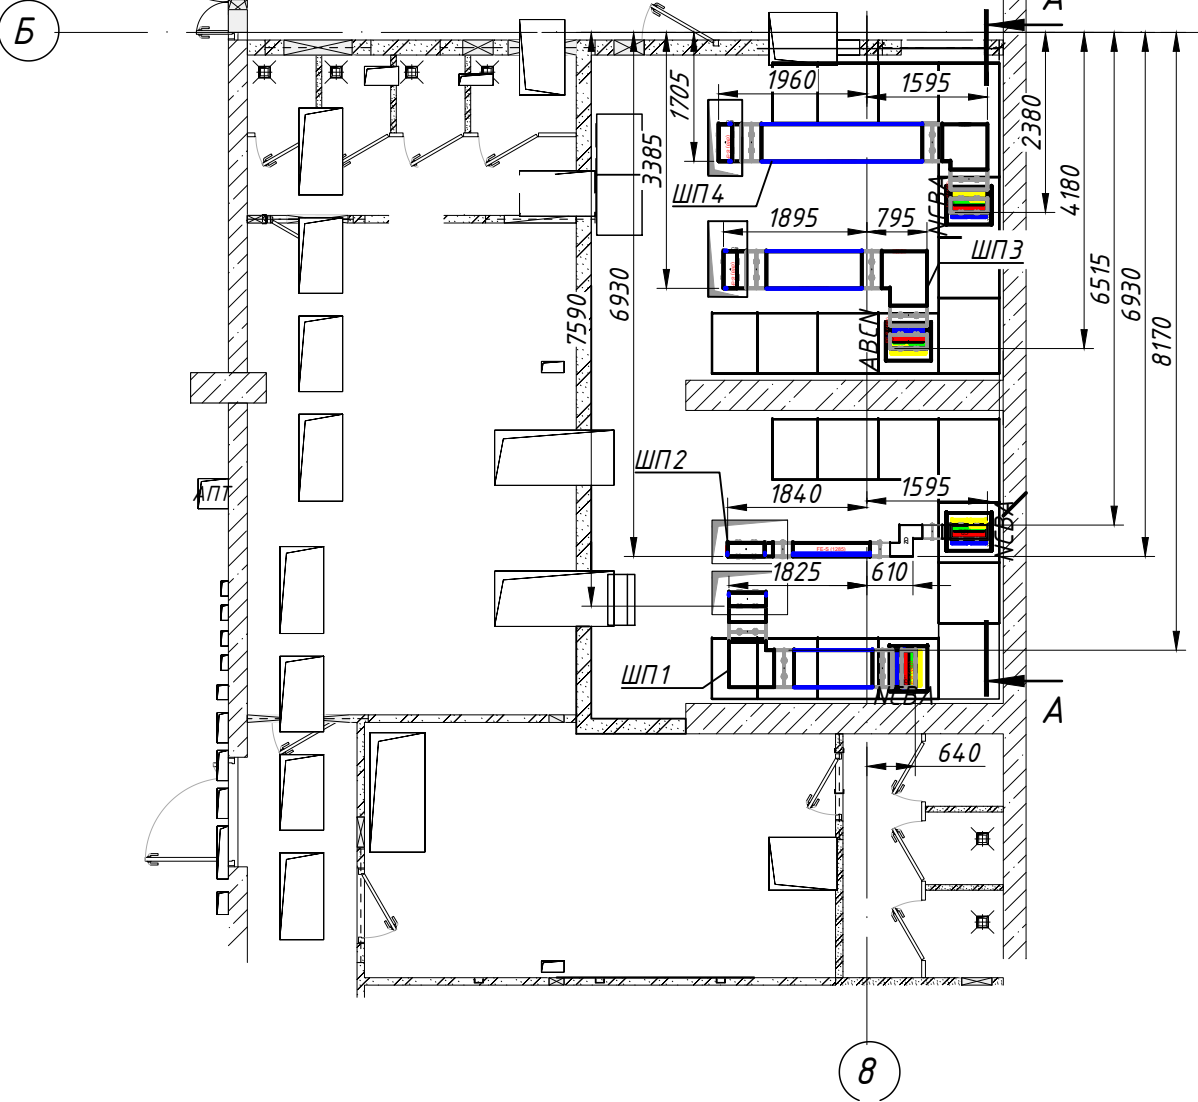


				___/___/___-ЭМ.ШП			
				г. Москва, ул. Наметкина д.10			
				Электрооборудование. Шинпровод.		Р	1
				Фрагменты плана прокладки шинпровода			

Фрагмент плана прокладки шинпровода в осях Ж/4-Б / 8/4-10/4
отм. -1,600

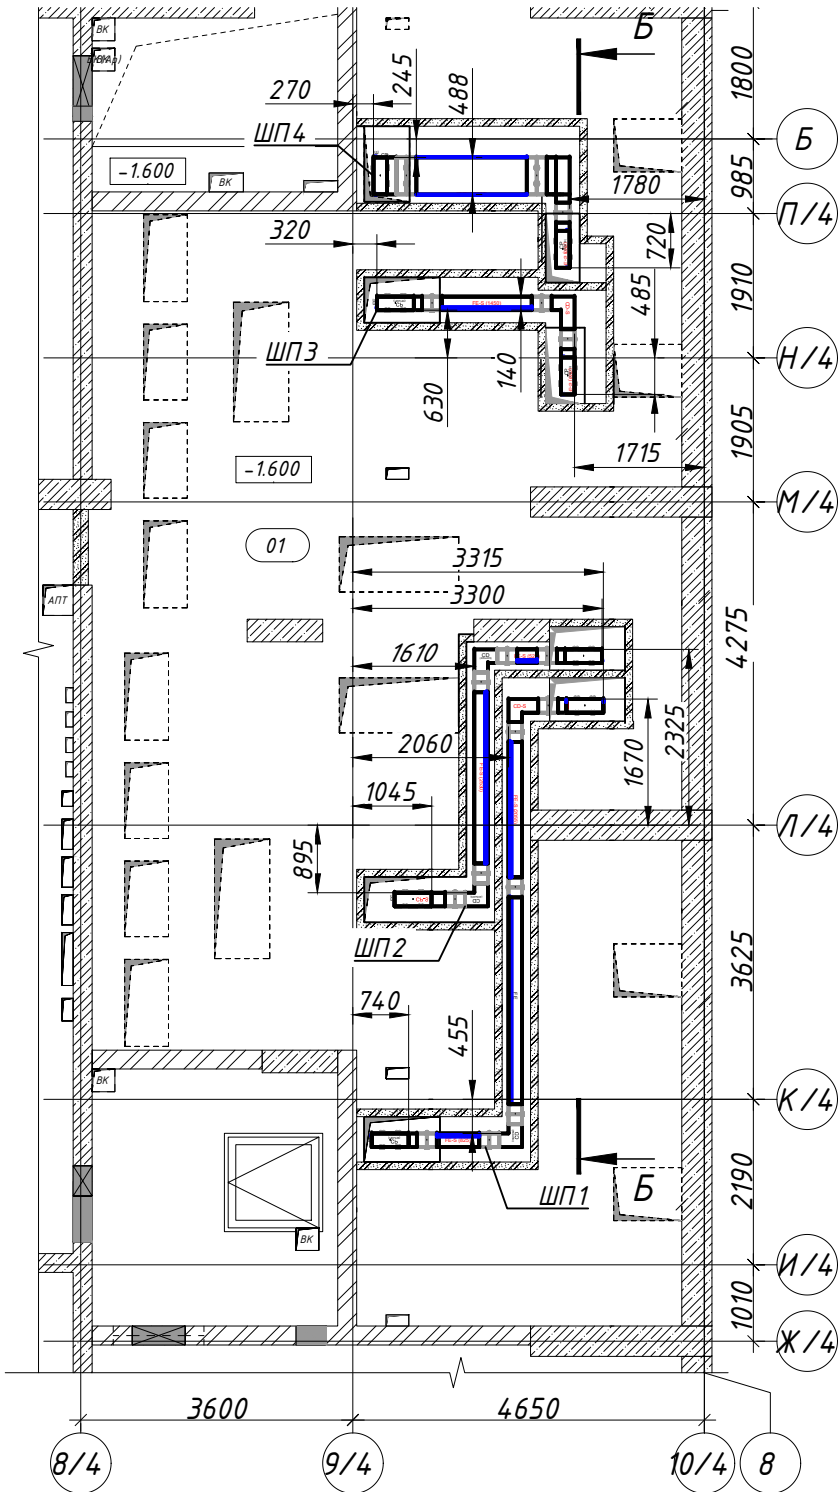

Фрагмент плана прокладки шинпровода
в осях Ж/4-Р/4 / 8/4-10/4 отм. +0,490

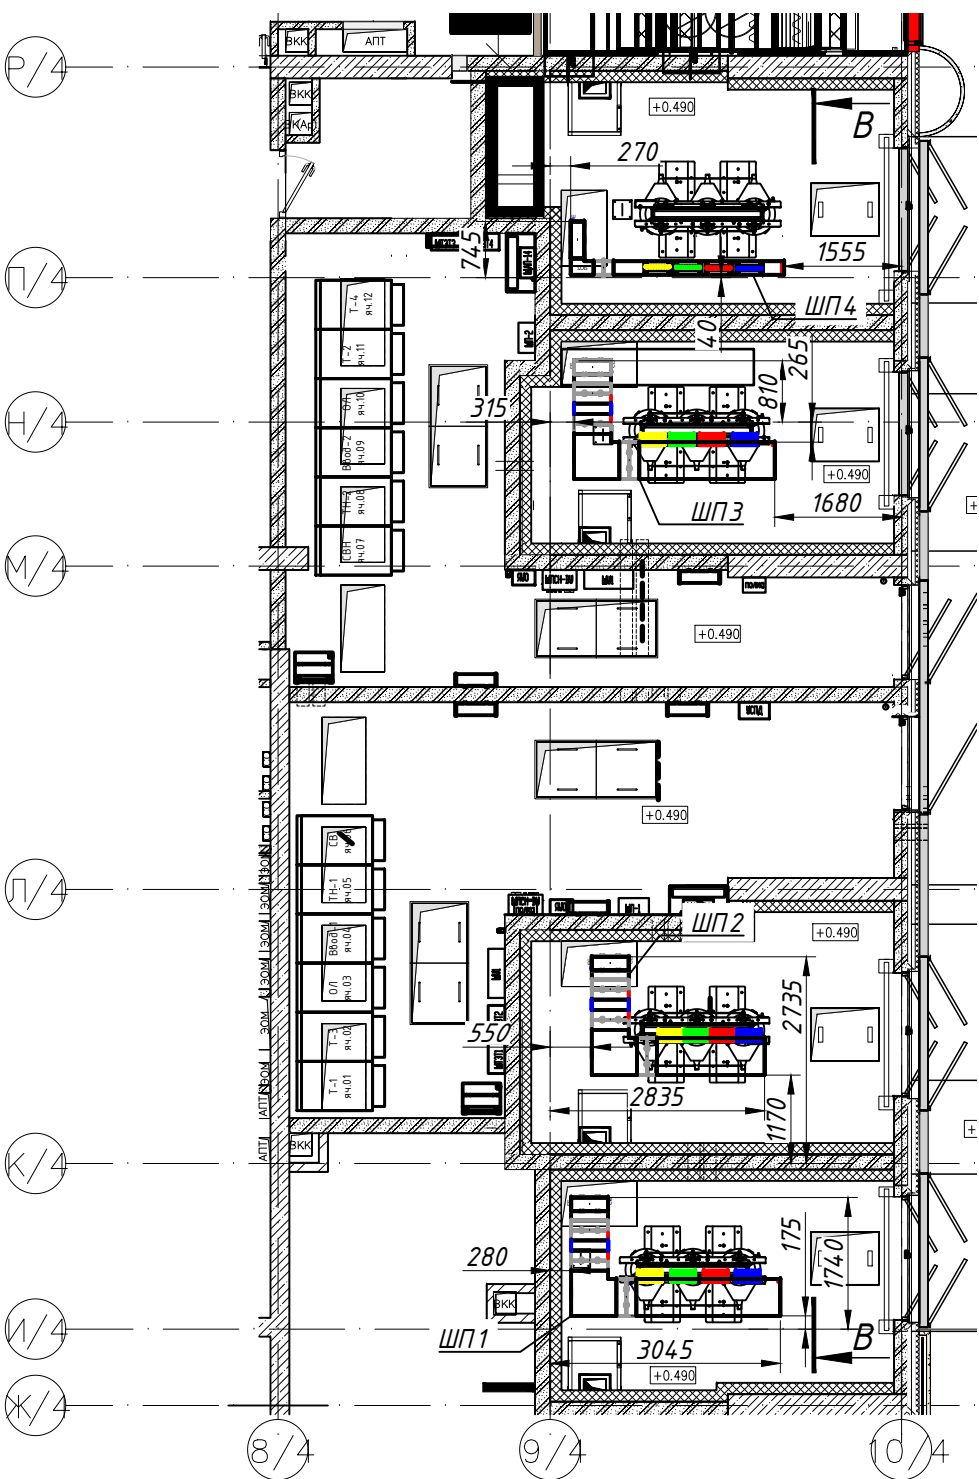

Условные обозначения

ШП1 - обозначение линии шинпровода KLM-S-40-AI-55-4-V3;
ШП2 - обозначение линии шинпровода KLM-S-40-AI-55-4-V3;
ШП3 - обозначение линии шинпровода KLM-S-40-AI-55-4-V3;
ШП4 - обозначение линии шинпровода KLM-S-40-AI-55-4-V3;

Примечания

- Порядок сборки линий шинпровода определяется последовательностью элементов в сборочной таблице;
- Монтаж шинпроводной линии осуществлять в соответствии с инструкцией по монтажу;
- Элементы крепежа шинпровода следует размещать таким образом, чтобы стыковочные элементы не несли механической нагрузки;
- Высотные отметки указаны от нижней грани шинпровода;
- Указанные размеры ориентировочные. Габариты шинпровода (ВхШ): KLM-S-40-AI-55-4-V3 - 488x140мм
- Высотные отметки указаны в абсолютных координатах;

Приложение № 9 к Договору поставки
№ МК2507/18 от 08.07.2025

СОГЛАСОВАНО
ООО "МК Инжиниринг"
Генеральный директор
_____/Карпова М. И./

М.П.

СОГЛАСОВАНО
ТОО "Айтек"
_____/Виноградов К. П./

М.П.

_____/_____/_____-ЭМ.ШП

г. Москва, ул. Наметкина д.10

Электрооборудование. Шинпровод.

Р

2

Передан через Диадок 17.07.2025 10:48 GMT+03:00
с7ace405-adc8-4bf7-8228-9f6cc4976f55
Фрагменты плана прокладки шинпровода






СОГЛАСОВАНО
ООО "МК Инжиниринг"
Генеральный директор
_____/Карпова М. И./
_____/_____/_____/

М.П.

СОГЛАСОВАНО
ООО "Айтек"
_____/Виноградов К. П./
_____/_____/_____/

М.П.

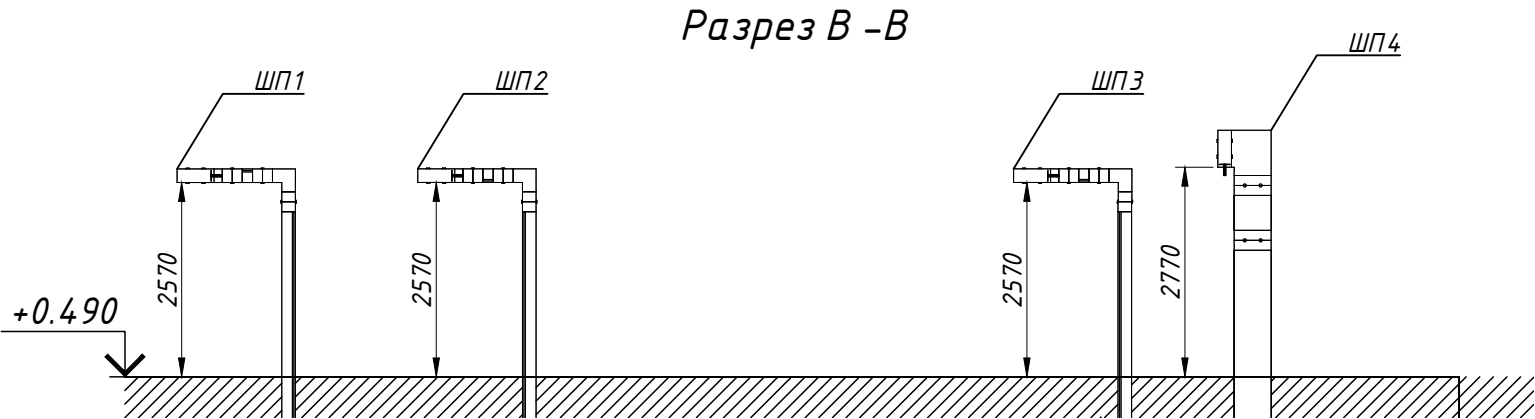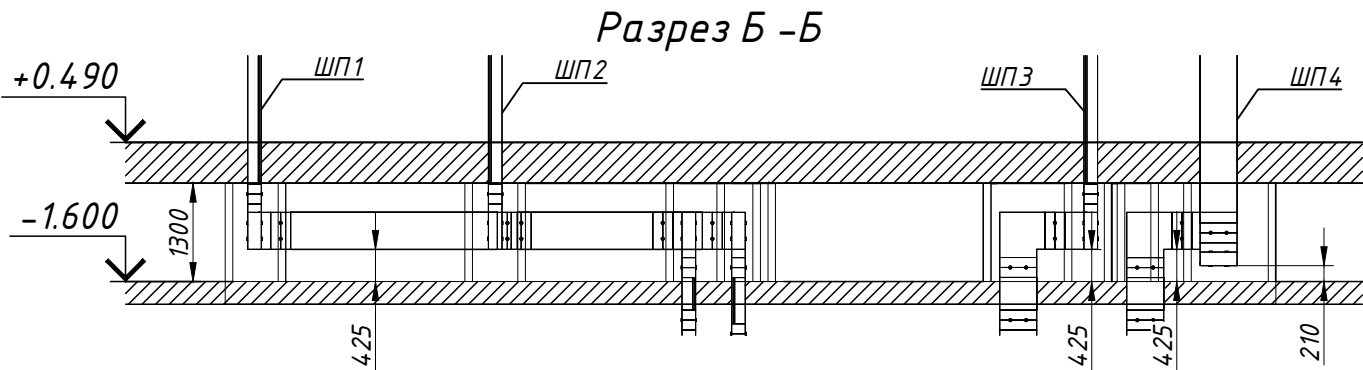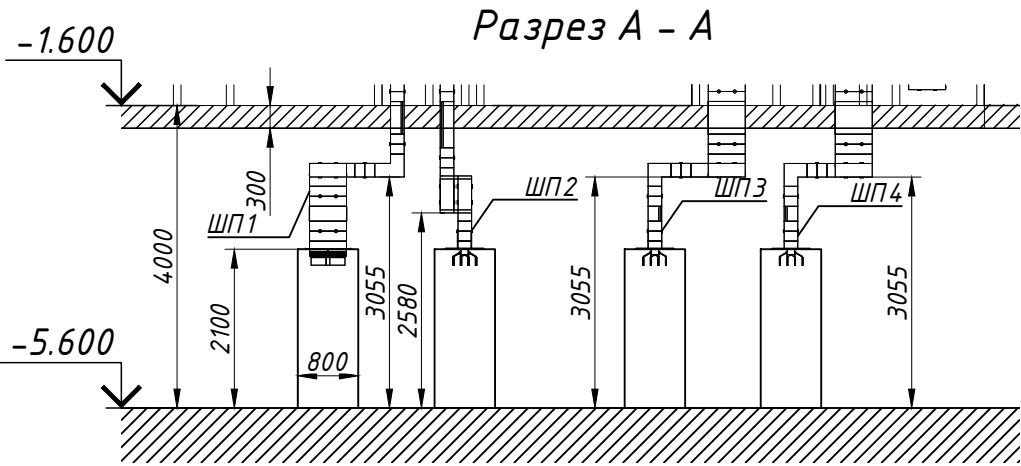

Условные обозначения

ШП1 - обозначение линии шинпровода KLM-S-40-AI-55-4-V3;
ШП2 - обозначение линии шинпровода KLM-S-40-AI-55-4-V3;
ШП3 - обозначение линии шинпровода KLM-S-40-AI-55-4-V3;
ШП4 - обозначение линии шинпровода KLM-S-40-AI-55-4-V3;

Примечания

- Порядок сборки линий шинпровода определяется последовательностью элементов в сборочной таблице;
- Монтаж шинпроводной линии осуществлять в соответствии с инструкцией по монтажу;
- Элементы крепежа шинпровода следует размещать таким образом, чтобы стыковочные элементы не несли механической нагрузки;
- Высотные отметки указаны от нижней грани шинпровода;
- Указанные размеры ориентировочные. Габариты шинпровода (ВхШ): KLM-S-40-AI-55-4-V3 - 488x140мм
- Высотные отметки указаны в абсолютных координатах;

						___/___/___-ЭМ.ШП			
						г. Москва, ул. Наметкина д.10			
						Электрооборудование. Шинпровод.	Р	З	
						Разрез А	Передан через Диадок 17.07.2025 10:48 GMT+03:00 с7ace405-adc8-4bf7-8228-9f6cc4976f55 Страница 63 из 69		
							ООО "ЛАВПРОЕКТ"		

АксонOMETрический вид линий шинопровода


Приложение № 9 к Договору поставки
№ МК2507/18 от 08.07.2025

СОГЛАСОВАНО
ООО "МК Инжиниринг"
Генеральный директор
_____/Карпова М. И./
_____/_____/_____/

М.П.

СОГЛАСОВАНО
ТОО "Айтек"
_____/Виноградов К. П./
_____/_____/_____/

М.П.

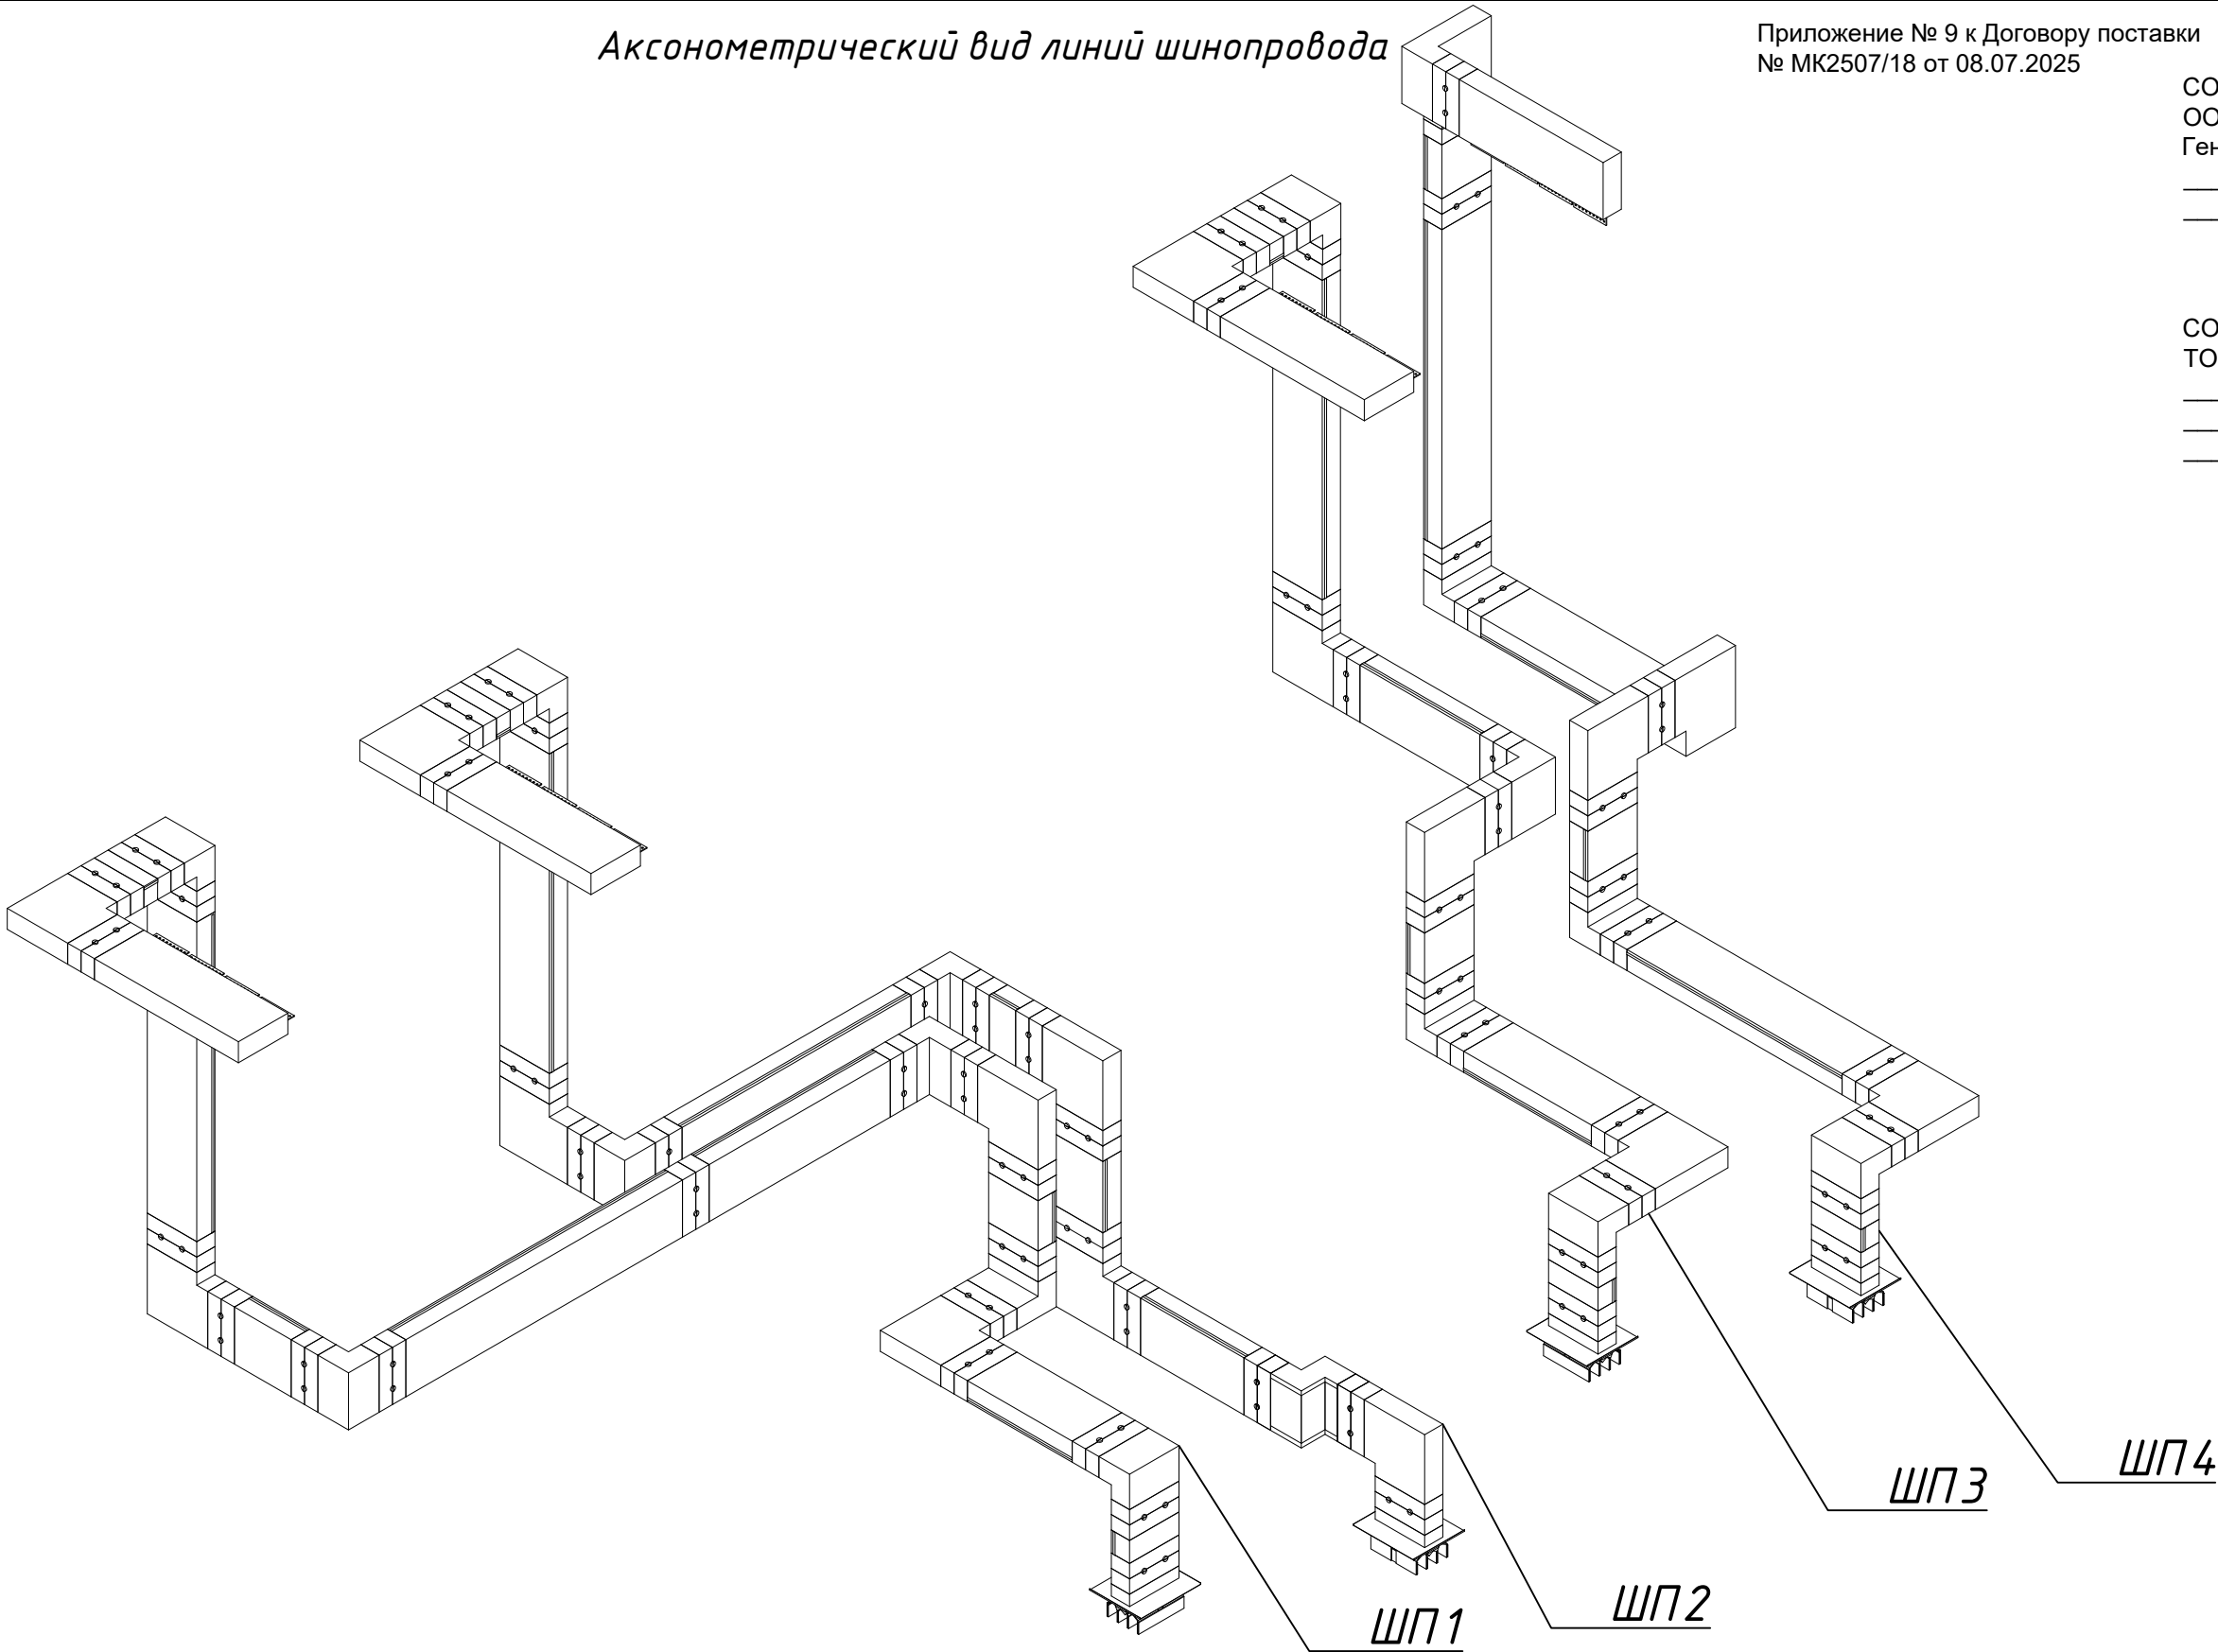

Условные обозначения
ШП1 – обозначение линии шинопровода KLM-S-40-AI-55-4-V3;
ШП2 – обозначение линии шинопровода KLM-S-40-AI-55-4-V3;
ШП3 – обозначение линии шинопровода KLM-S-40-AI-55-4-V3;
ШП4 – обозначение линии шинопровода KLM-S-40-AI-55-4-V3;

						___/___/___-ЭМ.ШП		
						г. Москва, ул. Наметкина д.10		
						Электрооборудование. Шинопровод.		
						Р	6	
						Передан через Диадок 17.07.2025 10:48 GMT+03:00 с7асе405-аdс8-4b77-8228-9fесс4976f55 АксонOMETрический вид линий шинопровода Страница 62 из 69		




СОГЛАСОВАНО
ООО "МК Инжиниринг"
Генеральный директор
_____/Карпова М. И./
_____/_____/_____/

М.П.

СОГЛАСОВАНО
ООО "Айтек"
_____/Виноградов К. П./
_____/_____/_____/

М.П.

АксонOMETрический вид линии шинопровода ШП1

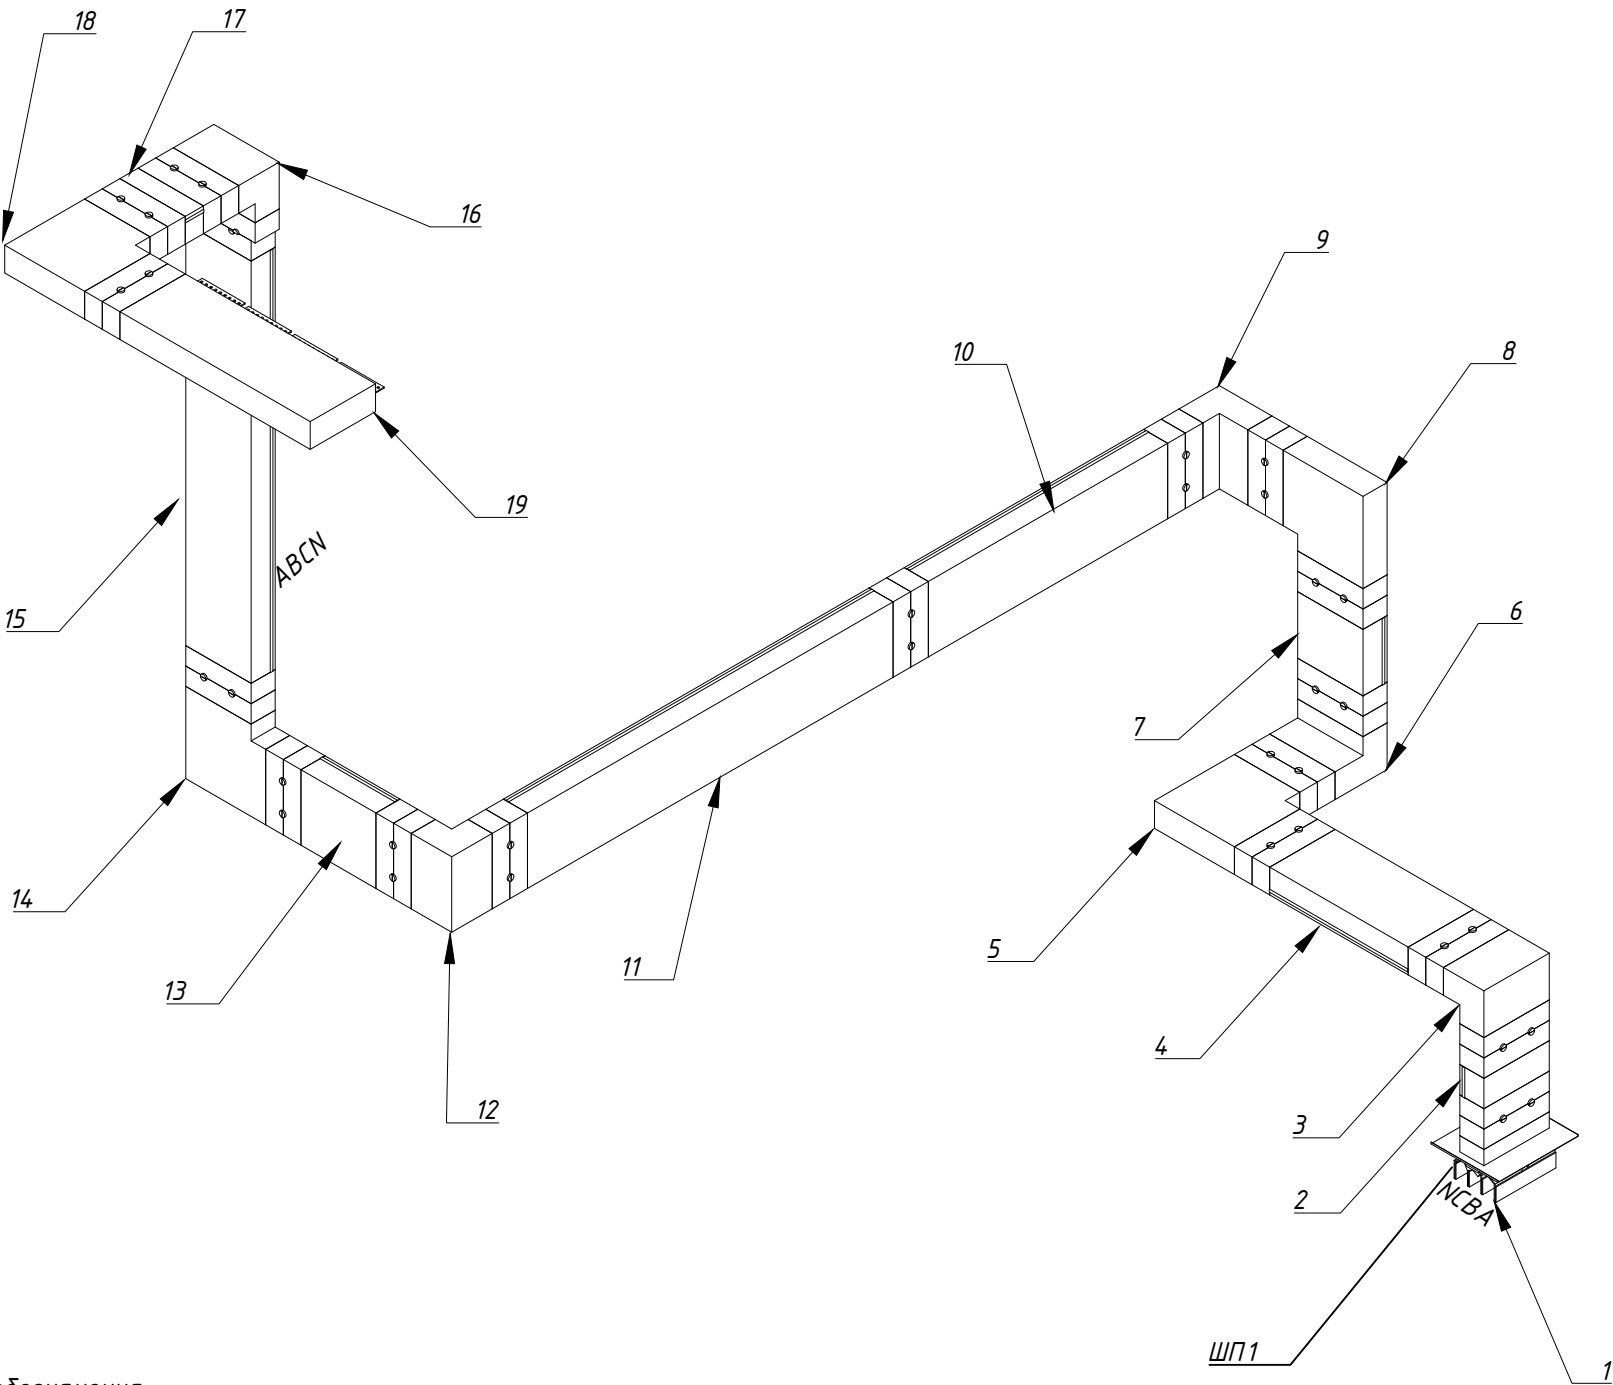

Сборочная таблица ШП1

ШП1			
№	Артикул	Длина, мм	Доп
1	KLM-S-40-AI-55-4-V3-ATSC	237	
2	KLM-S-40-AI-55-4-V3-FE-S1	460	
3	KLM-S-40-AI-55-4-V3-CD	435x435	
4	KLM-S-40-AI-55-4-V3-FE-S2	1300	Дозам.
5	KLM-S-40-AI-55-4-V3-CP	730x730	
6	KLM-S-40-AI-55-4-V3-CD-S1	520x435	
7	KLM-S-40-AI-55-4-V3-FE-S1	695	Дозам.
8	KLM-S-40-AI-55-4-V3-CP	730x730	
9	KLM-S-40-AI-55-4-V3-CD-S1	525x435	
10	KLM-S-40-AI-55-4-V3-FE-S3	2055	Дозам.
11	KLM-S-40-AI-55-4-V3-FE	3000	
12	KLM-S-40-AI-55-4-V3-CD	435x435	
13	KLM-S-40-AI-55-4-V3-FE-S1	825	Дозам.
14	KLM-S-40-AI-55-4-V3-CP	730x730	
15	KLM-S-40-AI-55-4-V3-FE	3000	Дозам.
16	KLM-S-40-AI-55-4-V3-CD	435x435	
17	KLM-S-40-AI-55-4-V3-FE-S1	400	
18	KLM-S-40-AI-55-4-V3-CP	730x730	
19	KLM-S-40-AI-55-4-V3-ATT		

Условные обозначения
ШП1 - обозначение линии шинопровода KLM-S-40-AI-55-4-V3;
ШП2 - обозначение линии шинопровода KLM-S-40-AI-55-4-V3;
ШП3 - обозначение линии шинопровода KLM-S-40-AI-55-4-V3;
ШП4 - обозначение линии шинопровода KLM-S-40-AI-55-4-V3;
ATSC - Терминальная секция стандартная
ATT - Терминальная секция трансформаторная
CD - Угол горизонтальный стандартный
CP - Угол вертикальный стандартный
CD-S1 - Нестандартный горизонтальный угол
CP-S1 - Нестандартный вертикальный угол
FE - Прямая секция стандартного размера 3000мм
FE-S1 - Нестандартная прямая секция длиной от 500мм до 999мм
FE-S2 - Нестандартная прямая секция длиной от 1000мм до 1999мм
FE-S3 - Нестандартная прямая секция длиной от 2000мм до 2999мм
ZD - Z-образная горизонтальная секция торная
ZDP - Угол комбинированный

						___/___/___-ЭМ.ШП			
						г. Москва, ул. Наметкина д.10			
						Электрооборудование. Шинопровод.	P	5	
							Передан через Диадок 17.07.2025 10:48 GMT+03:00 с7ace405-adc8-4bf7-8228-9f6cc4976f55 Страница 65 из 69		
						АксонOMETрический вид линии шинопроводов ШП1	ООО "ЛАВЕНРОСТ"		

Аксонетрический вид линии шинпровода ШП2


Приложение № 9 к Договору поставки
№ МК2507/18 от 08.07.2025

СОГЛАСОВАНО
ООО "МК Инжиниринг"
Генеральный директор
_____/Карпова М. И./
_____/_____/_____/

М.П.

СОГЛАСОВАНО
ООО "Айтек"
_____/Виноградов К. П./
_____/_____/_____/

М.П.

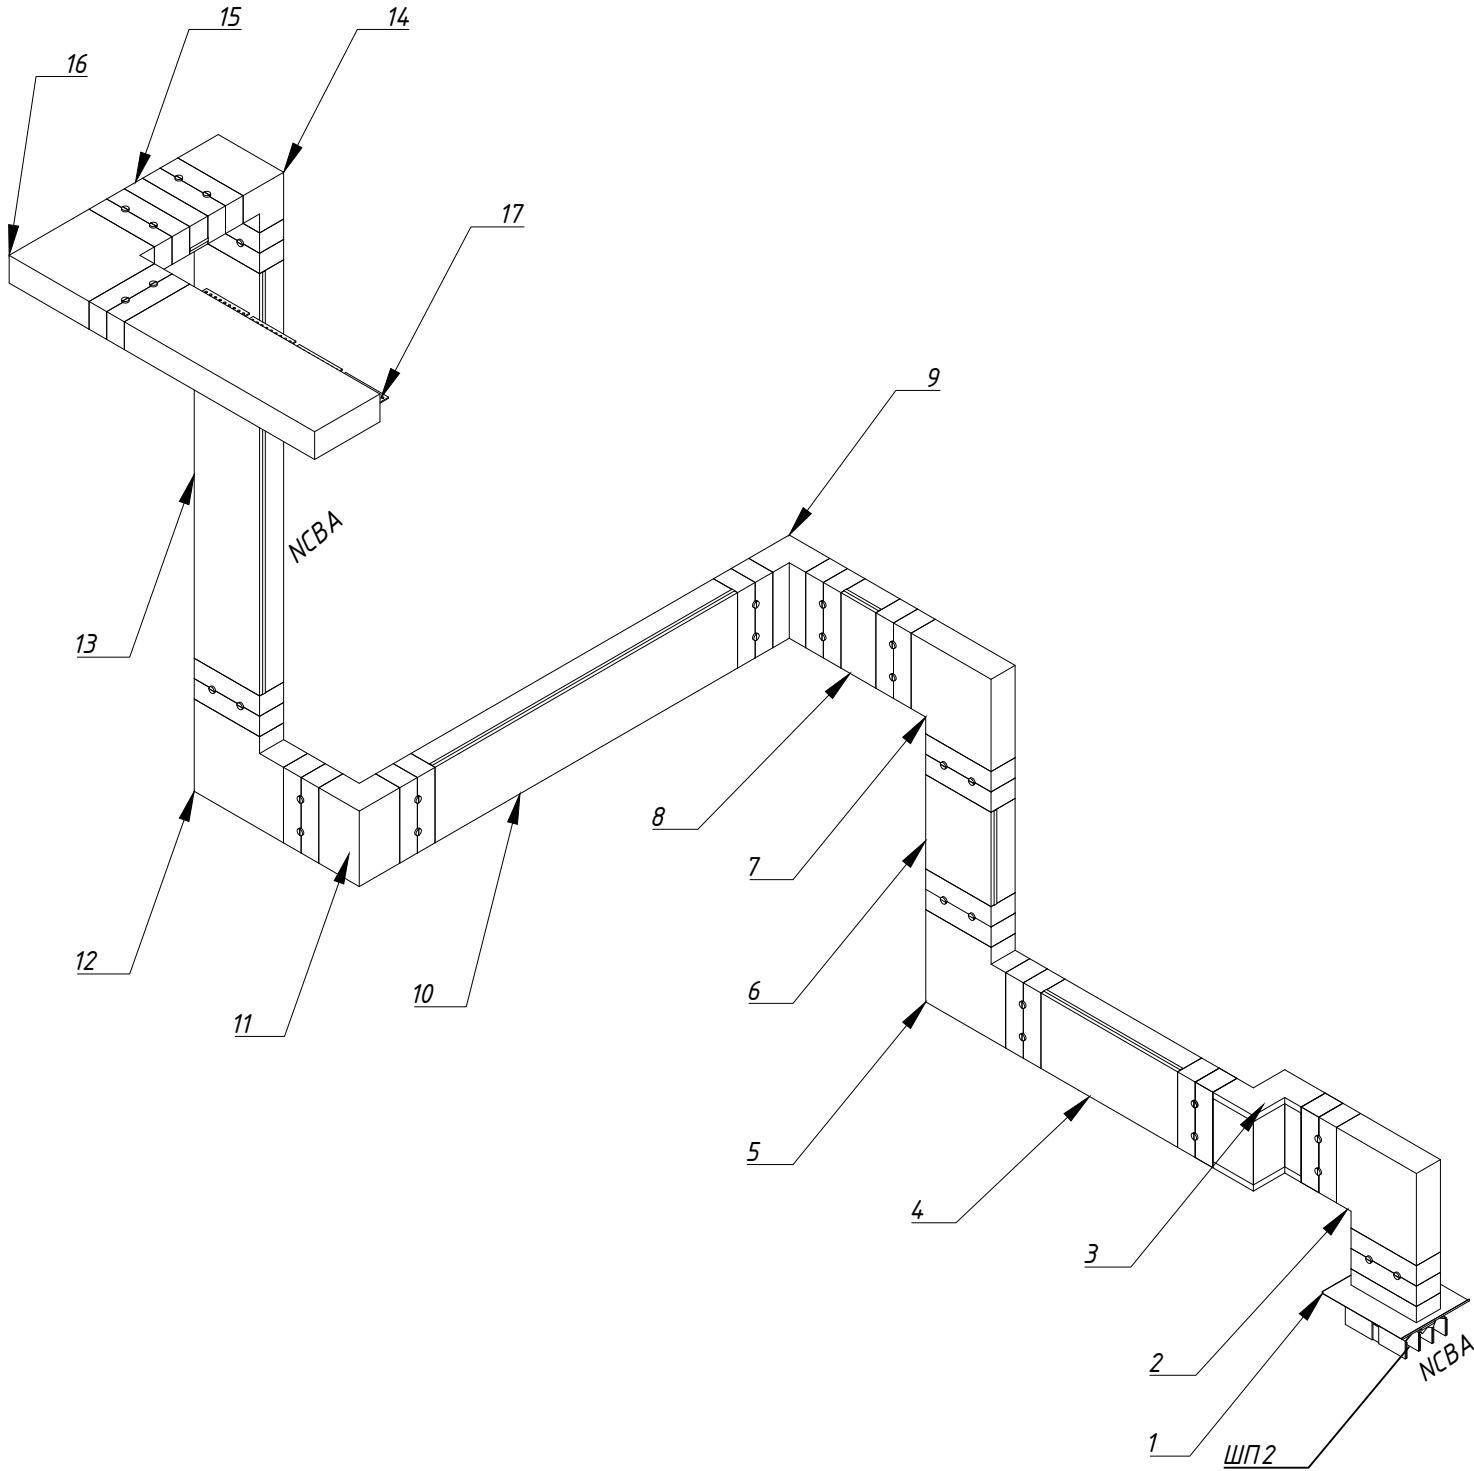

Сборочная таблица ШП2

ШП2			
№	Артикул	Длина, мм	Доп
1	KLM-S-40-AI-55-4-V3-ATSC	237	
2	KLM-S-40-AI-55-4-V3-CP	730x730	
3	KLM-S-40-AI-55-4-V3-ZD	435x415x435	
4	KLM-S-40-AI-55-4-V3-FE-S2	1285	Дозам
5	KLM-S-40-AI-55-4-V3-CP	730x730	
6	KLM-S-40-AI-55-4-V3-FE-S1	875	Дозам
7	KLM-S-40-AI-55-4-V3-CP	730x730	
8	KLM-S-40-AI-55-4-V3-FE-S1	525	
9	KLM-S-40-AI-55-4-V3-CD	435x435	
10	KLM-S-40-AI-55-4-V3-FE-S2	2530	Дозам
11	KLM-S-40-AI-55-4-V3-CD	435x435	
12	KLM-S-40-AI-55-4-V3-CP	800x730	
13	KLM-S-40-AI-55-4-V3-FE	3000	Дозам
14	KLM-S-40-AI-55-4-V3-CD	435x435	
15	KLM-S-40-AI-55-4-V3-FE-S1	400	
16	KLM-S-40-AI-55-4-V3-CP	730x730	
17	KLM-S-40-AI-55-4-V3-ATT		

Условные обозначения
ШП1 - обозначение линии шинпровода KLM-S-40-AI-55-4-V3;
ШП2 - обозначение линии шинпровода KLM-S-40-AI-55-4-V3;
ШП3 - обозначение линии шинпровода KLM-S-40-AI-55-4-V3;
ШП4 - обозначение линии шинпровода KLM-S-40-AI-55-4-V3;
ATSC - Терминальная секция стандартная
ATT - Терминальная секция трансформаторная
CD - Угол горизонтальный стандартный
CP - Угол вертикальный стандартный
CD-S1 - Нестандартный горизонтальный угол
CP-S1 - Нестандартный вертикальный угол
FE - Прямая секция стандартного размера 3000мм
FE-S1 - Нестандартная прямая секция длиной от 500мм до 999мм
FE-S2 - Нестандартная прямая секция длиной от 1000мм до 1999мм
FE-S3 - Нестандартная прямая секция длиной от 2000мм до 2999мм
ZD - Z-образная горизонтальная секция
ZDP - Угол комбинированный

						___/___/___-ЭМ.ШП			
						г. Москва, ул. Наметкина д.10			
						Электрооборудование. Шинопровод.	Р	5	
						Аксонотрический вид линии шинопровода ШП2	Передан через Диадок 17.07.2025 10:48 GMT+03:00 с7ace405-adc8-4bf7-8228-9f6cc4976f55 Страница 60 из 69		
							ООО "МК ИНЖИНИРИНГ" 		


СОГЛАСОВАНО
ООО "МК Инжиниринг"
Генеральный директор
_____/Карпова М. И./
_____/_____/_____/

М.П.

СОГЛАСОВАНО
ООО "Айтек"
_____/Виноградов К. П./
_____/_____/_____/

М.П.

АксонOMETрический вид линии шинопровода ШПЗ

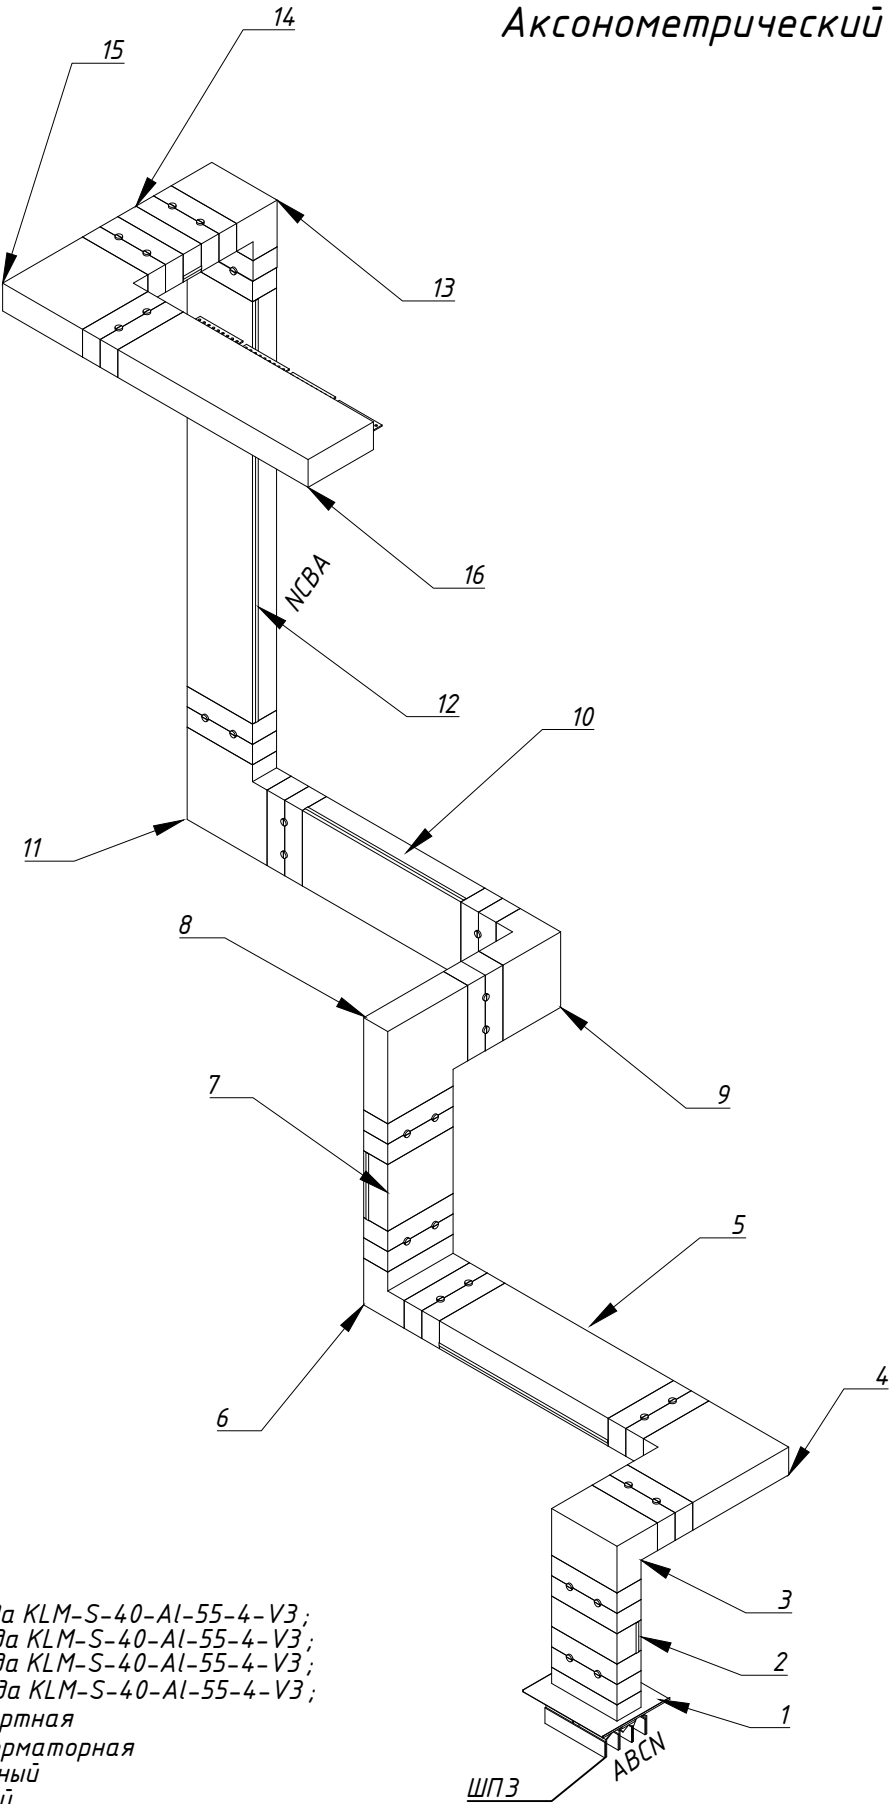

Сборочная таблица ШПЗ

ШПЗ			
№	Артикул	Длина, мм	Доп
1	KLM-S-40-AI-55-4-V3-ATSC	237	
2	KLM-S-40-AI-55-4-V3-FE-S1	460	Дозам
3	KLM-S-40-AI-55-4-V3-CD	435x435	
4	KLM-S-40-AI-55-4-V3-CP-S1	730x850	
5	KLM-S-40-AI-55-4-V3-FE-S2	1525	Дозам
6	KLM-S-40-AI-55-4-V3-CD	435x435	
7	KLM-S-40-AI-55-4-V3-FE-S1	695	
8	KLM-S-40-AI-55-4-V3-CP	730x730	
9	KLM-S-40-AI-55-4-V3-CD-S1	565x435	
10	KLM-S-40-AI-55-4-V3-FE-S2	1450	Дозам
11	KLM-S-40-AI-55-4-V3-CP	730x730	
12	KLM-S-40-AI-55-4-V3-FE	3000	Дозам
13	KLM-S-40-AI-55-4-V3-CD	435x435	
14	KLM-S-40-AI-55-4-V3-FE-S1	400	
15	KLM-S-40-AI-55-4-V3-CP	730x730	
16	KLM-S-40-AI-55-4-V3-ATT		

Условные обозначения
ШП1 - обозначение линии шинопровода KLM-S-40-AI-55-4-V3;
ШП2 - обозначение линии шинопровода KLM-S-40-AI-55-4-V3;
ШП3 - обозначение линии шинопровода KLM-S-40-AI-55-4-V3;
ШП4 - обозначение линии шинопровода KLM-S-40-AI-55-4-V3;
ATSC - Терминальная секция стандартная
ATT - Терминальная секция трансформаторная
CD - Угол горизонтальный стандартный
CP - Угол вертикальный стандартный
CD-S1 - Нестандартный горизонтальный угол
CP-S1 - Нестандартный вертикальный угол
FE - Прямая секция стандартного размера 3000мм
FE-S1 - Нестандартная прямая секция длиной от 500мм до 999мм
FE-S2 - Нестандартная прямая секция длиной от 1000мм до 1999мм
FE-S3 - Нестандартная прямая секция длиной от 2000мм до 2999мм
ZD - Z-образная горизонтальная секция торная
ZDP - Угол комбинированный

						___/___/___-ЭМ.ШП			
						г. Москва, ул. Наметкина д.10			
						Электрооборудование. Шинопровод.			
							Р	4	
						АксонOMETрический вид линии шинопровода ШПЗ	Передан через Диадок 17.07.2025 10:48 GMT+03:00 с7ace405-adc8-4bf7-8228-9fccc4976f55 Страница 6 из 69		
							ООО "АЙТЕК" 		


СОГЛАСОВАНО
ООО "МК Инжиниринг"
Генеральный директор
_____/Карпова М. И./
_____/_____/_____/

М.П.

СОГЛАСОВАНО
ООО "Айтек"
_____/Виноградов К. П./
_____/_____/_____/

М.П.

АксонOMETрический вид линии шинопровода ШП4

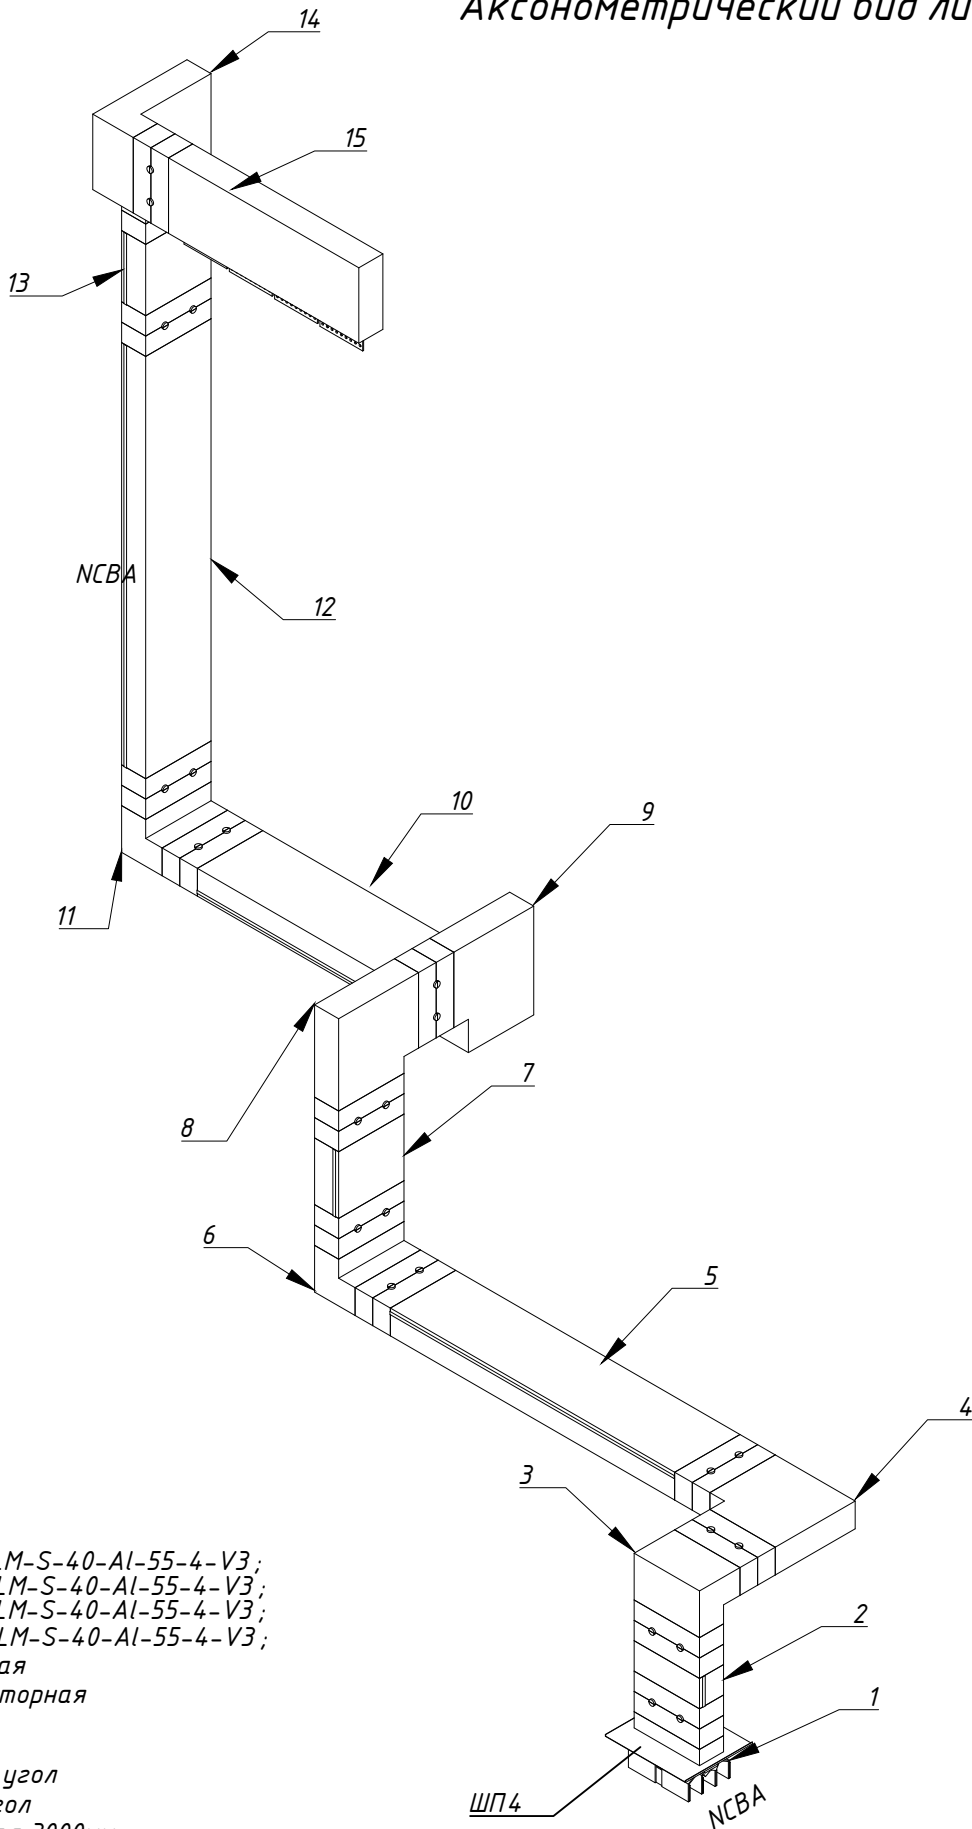

Сборочная таблица ШП4

ШП4			
№	Артикул	Длина, мм	Доп
1	KLM-S-40-AI-55-4-V3-ATSC	237	
2	KLM-S-40-AI-55-4-V3-FE-S1	460	Дозам.
3	KLM-S-40-AI-55-4-V3-CD	435x435	
4	KLM-S-40-AI-55-4-V3-CP	730x730	
5	KLM-S-40-AI-55-4-V3-FE-S3	2390	Дозам.
6	KLM-S-40-AI-55-4-V3-CD	435x435	
7	KLM-S-40-AI-55-4-V3-FE-S1	692	
8	KLM-S-40-AI-55-4-V3-CP	730x730	
9	KLM-S-40-AI-55-4-V3-ZDP	730x700x435	
10	KLM-S-40-AI-55-4-V3-FE-S2	1725	Дозам.
11	KLM-S-40-AI-55-4-V3-CD	435x435	
12	KLM-S-40-AI-55-4-V3-FE	3000	
13	KLM-S-40-AI-55-4-V3-FE-S1	725	Дозам.
14	KLM-S-40-AI-55-4-V3-ZDP	730x700x435	
15	KLM-S-40-AI-55-4-V3-ATT		

Условные обозначения

ШП1 - обозначение линии шинопровода KLM-S-40-AI-55-4-V3;
ШП2 - обозначение линии шинопровода KLM-S-40-AI-55-4-V3;
ШП3 - обозначение линии шинопровода KLM-S-40-AI-55-4-V3;
ШП4 - обозначение линии шинопровода KLM-S-40-AI-55-4-V3;
ATSC - Терминальная секция стандартная
ATT - Терминальная секция трансформаторная
CD - Угол горизонтальный стандартный
CP - Угол вертикальный стандартный
CD-S1 - Нестандартный горизонтальный угол
CP-S1 - Нестандартный вертикальный угол
FE - Прямая секция стандартного размера 3000мм
FE-S1 - Нестандартная прямая секция длиной от 500мм до 999мм
FE-S2 - Нестандартная прямая секция длиной от 1000мм до 1999мм
FE-S3 - Нестандартная прямая секция длиной от 2000мм до 2999мм
ZD - Z-образная горизонтальная секция торная
ZDP - Угол комбинированный

						___/___/___-ЭМ.ШП			
						г. Москва, ул. Наметкина д.10			
						Электрооборудование. Шинопровод.		Р	4
						АксонOMETрический вид линии шинопровода ШП4		Передан через Диадок 17.07.2025 10:48 GMT+03:00 с7ace405-adc8-4bf7-8228-9fccc4976f55 Страница 63 из 69	



Документ подписан и передан через оператора ЭДО АО «ПФ «СБ Контур»

	Организация, сотрудник		Доверенность: рег. номер, период действия и статус		Сертификат: серийный номер, период действия	Дата и время подписания
Подписи отправителя:		ООО "АЙТЕК" ВИНОГРАДОВ КОНСТАНТИН ПЕТРОВИЧ, ГЕНЕРАЛЬНЫЙ ДИРЕКТОР		Не требуется для подписания	02832986002FB28F834C98203FD75A8358 с 21.11.2024 10:58 по 21.02.2026 10:58 GMT+03:00	17.07.2025 10:48 GMT+03:00 Подпись соответствует файлу документа
Подписи получателя:		ООО "МК-ИНЖИНИРИНГ" КАРПОВА МАРИЯ ИВАНОВНА, ГЕНЕРАЛЬНЫЙ ДИРЕКТОР		Не требуется для подписания	026C268800C9B2008945FB69464E77A7FF с 24.04.2025 11:05 по 24.07.2026 11:05 GMT+03:00	17.07.2025 11:40 GMT+03:00 Подпись соответствует файлу документа