
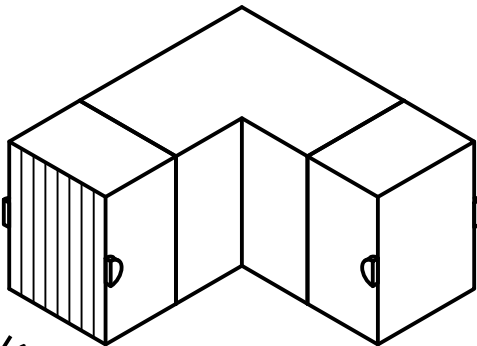


Согласовано					
Инов. № подл.	Подл. и дата	Взам. инв. №			

CD


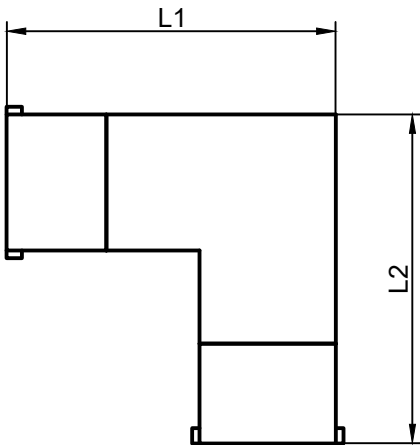


ABCN(PE) - v1
(PE)NCBA - v2
CBAN(PE) - v3
(PE)NABC - v4

Пример обозначения попок для хранения секций:
13.25.xxx.012.000-Vxx-L1xL2xL3
В случае добавления в секции типа, то наименование
следует принимать как:
13.25.xxx.012.000-Vxx-txx-L1xL2xL3

Разделитель между L - латинская 'x'.

CDSA

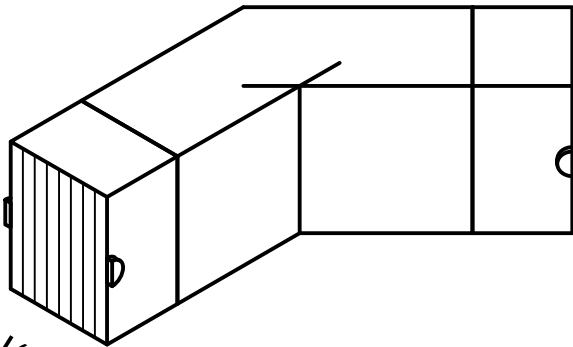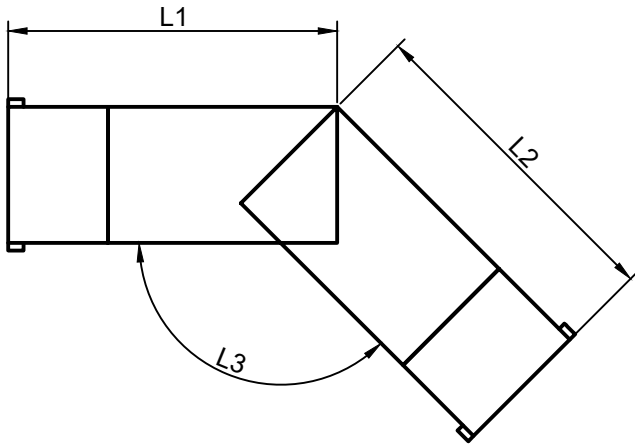



ABCN(PE) - v1
(PE)NCBA - v2
CBAN(PE) - v3
(PE)NABC - v4

1. Габаритные размеры указываются от оси стыка.

						Эскизы секций версия 7			
Изм.	Кол.уч	Лист	№ док.	Подп.	Дата	Секции шинопровода	Стадия	Лист	Листов
Разраб.		Елдин Е.В.			10.25		Р	1	7
Проверил		Банников Е.Д.			10.25				
									
Утвердил		Банников П.В.			10.25				



Согласовано					
Инов. № подл.	Подл. и дата		Взам. инв. №		

CP

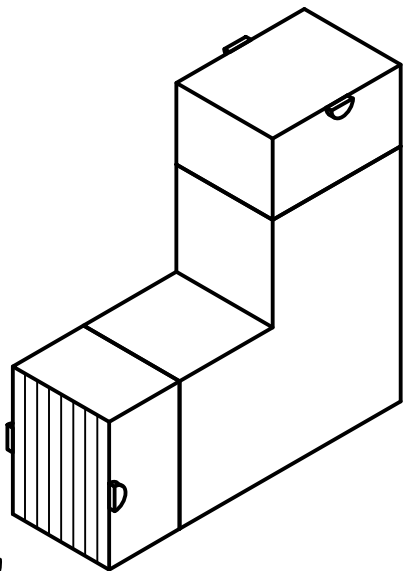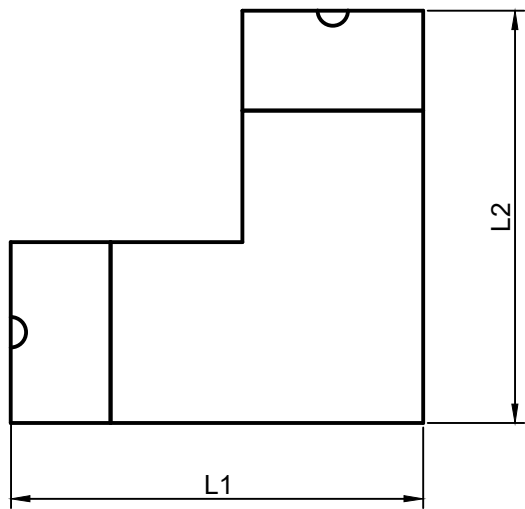

ABCN(PE) - v1
(PE)NCBA - v2
CBAN(PE) - v3
(PE)NABC - v4

CPSA

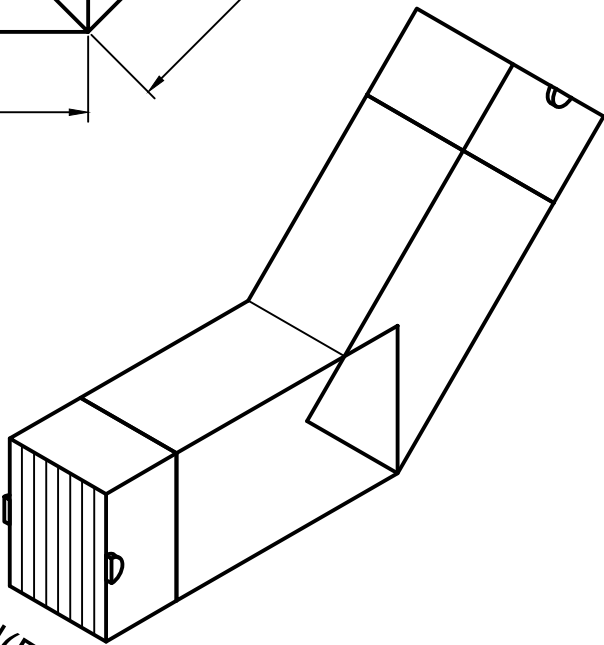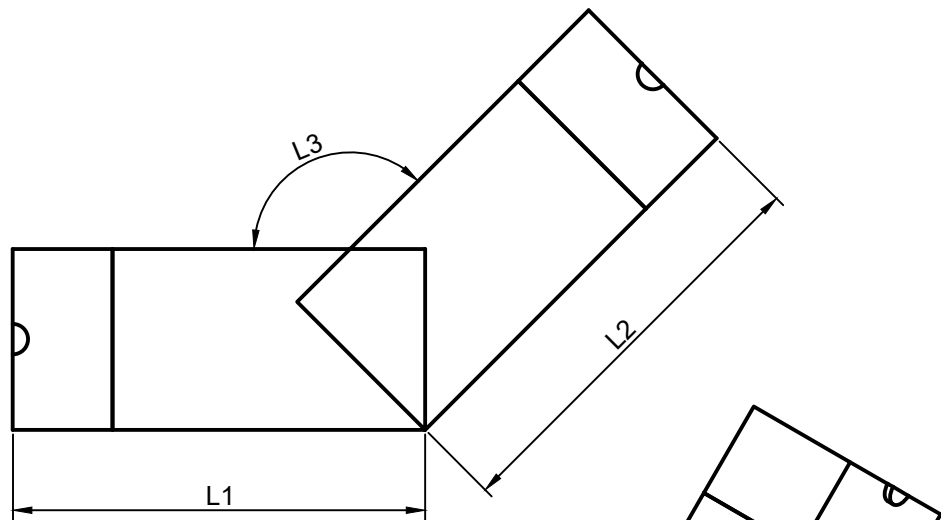

ABCN(PE) - v1
(PE)NCBA - v2
CBAN(PE) - v3
(PE)NABC - v4

Пример обозначения попок для хранения секций:
13.25.xxx.012.000-Vxx-L1xL2xL3
В случае добавления в секции типа, то наименование
следует принимать как:
13.25.xxx.012.000-Vxx-txx-L1xL2xL3



Разделитель между L - латинская 'x'.

1. Габаритные размеры указываются от оси стыка.

						Эскизы секций версия 7			
Изм.	Кол.уч	Лист	№ док.	Подп.	Дата	Секции шинопровода	Стадия	Лист	Листов
Разраб.		Елдин Е.В.			10.25		Р	2	7
Проверил		Банников Е.Д.			10.25				
									
Утвердил		Банников П.В.			10.25				



Согласовано					
Инов. № подл.	Подл. и дата		Взам. инв. №		

ZD

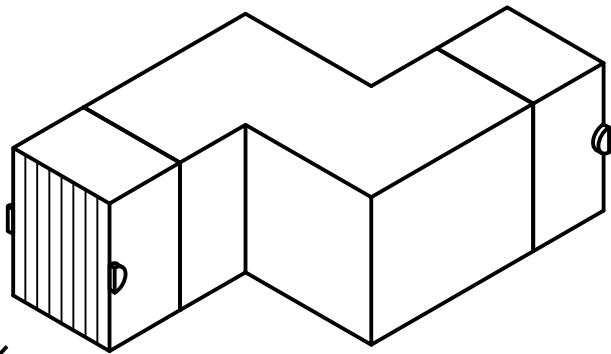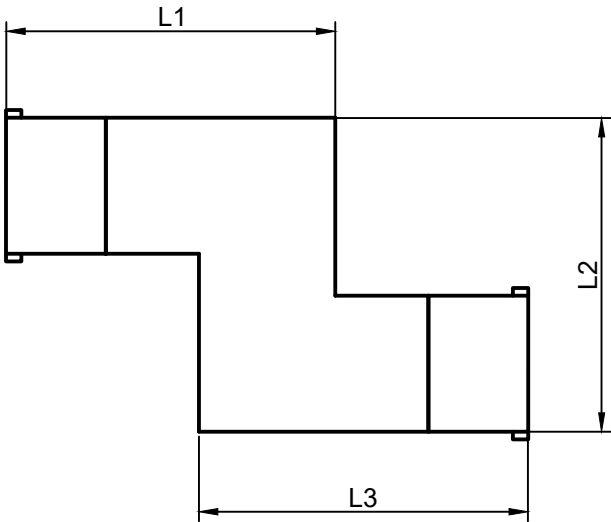

ABCN(PE) - v1
(PE)NCBA - v2
CBAN(PE) - v3
(PE)NABC - v4

ZP

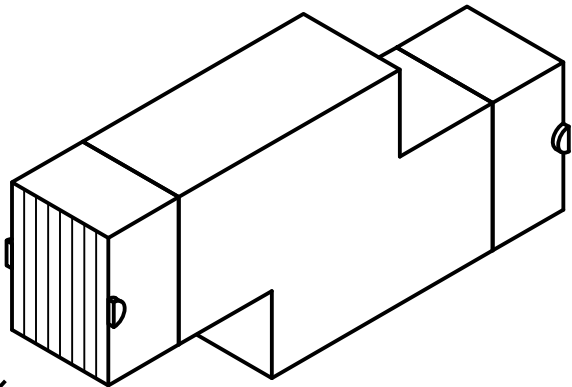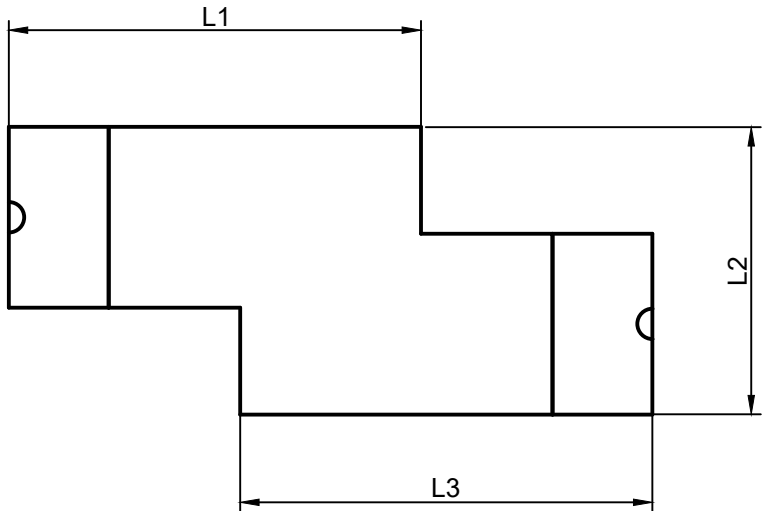

ABCN(PE) - v1
(PE)NCBA - v2
CBAN(PE) - v3
(PE)NABC - v4

Пример обозначения попок для хранения секций:
13.25.xxx.012.000-Vxx-L1xL2xL3
В случае добавления в секции типа, то наименование
следует принимать как:
13.25.xxx.012.000-Vxx-txx-L1xL2xL3

Разделитель между L - латинская 'x'.

1. Габаритные размеры указываются от оси стыка.

						-			
						Эскизы секций версия 7			
Изм.	Кол.уч	Лист	№ док.	Подп.	Дата	Секции шинопровода	Стадия	Лист	Листов
Разраб.		Елдин Е.В.			10.25		Р	3	7
Проверил		Банников Е.Д.			10.25				
									
Утвердил		Банников П.В.			10.25				



Согласовано

Взам. инв. №

Подл. и дата

Инв. № подл.

TP/TPS1

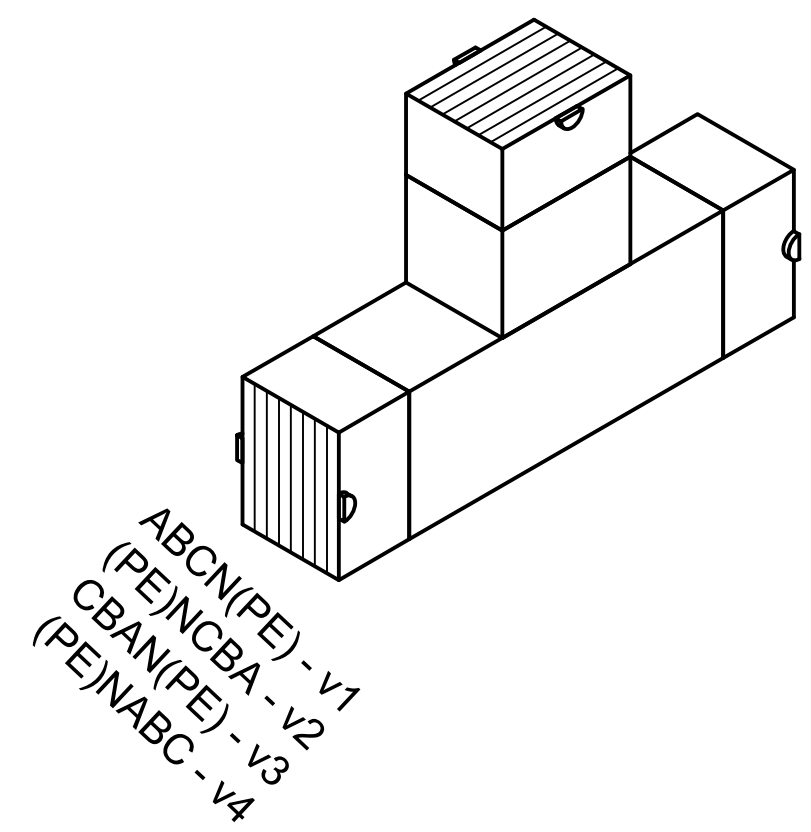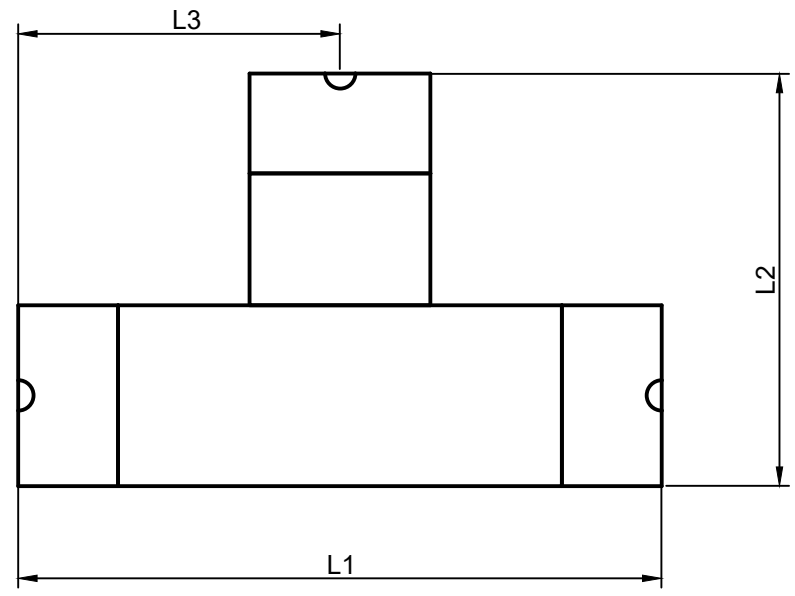



1. Габаритные размеры указываются от оси стыка.

Пример обозначения попок для хранения секций:
13.25.xxx.012.000-Vxx-L1xL2xL3
В случае добавления в секции типа, то наименование
следует принимать как:
13.25.xxx.012.000-Vxx-txx-L1xL2xL3

Разделитель между L - латинская 'x'.

						Эскизы секций версия 7			
Изм.	Кол.уч	Лист	№ док.	Подп.	Дата	Секции шинопровода	Стадия	Лист	Листов
Разраб.		Елдин Е.В.			10.25		Р	4	7
Проверил		Банников Е.Д.			10.25				
									
Утвердил		Банников П.В.			10.25				

ZDP

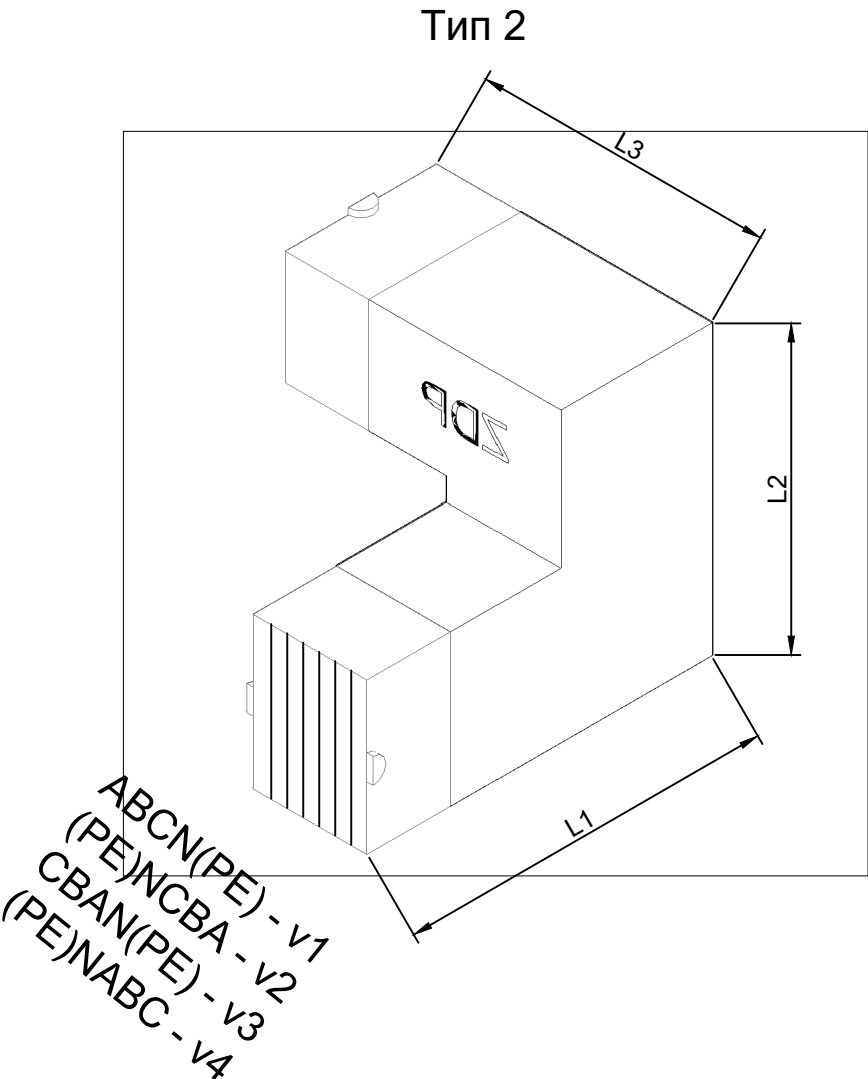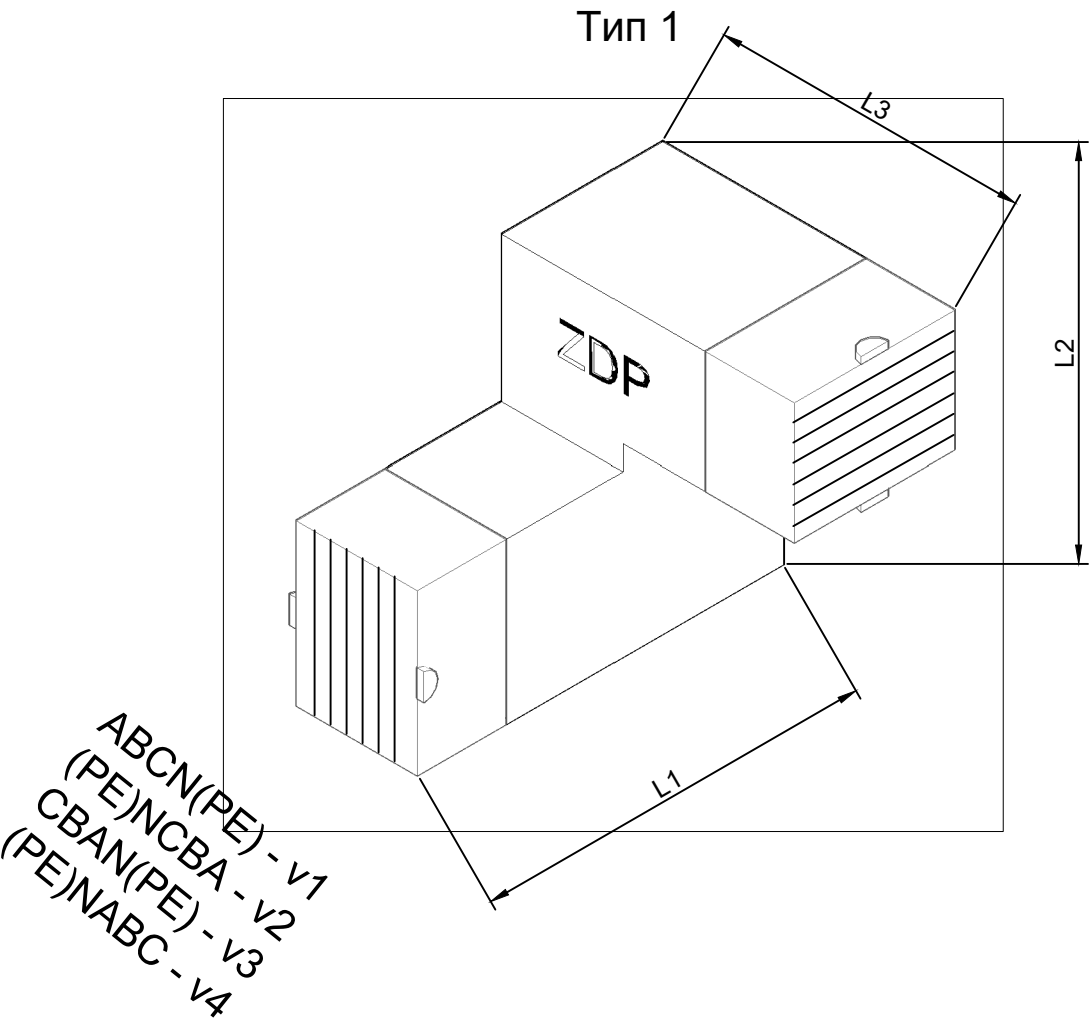

1. Габаритные размеры указываются от оси стыка.

Пример обозначения попок для хранения секций:
13.25.xxx.012.000-Vxx-L1xL2xL3
В случае добавления в секции типа, то наименование
следует принимать как:
13.25.xxx.012.000-Vxx-txx-L1xL2xL3

Разделитель между L - латинская 'x'.

						-			
						Эскизы секций версия 7			
Изм.	Кол.уч	Лист	№ док.	Подп.	Дата	Секции шинопровода	Стадия	Лист	Листов
Разраб.		Елдин Е.В.			10.25		Р	5	7
Проверил		Банников Е.Д.			10.25				
Утвердил		Банников П.В.			10.25				



Согласовано

Взам. инв. №

Подл. и дата

Инв. № подл.

№	фазировка с торца	фазировка на ответвлении	обозначение
1	ABCN(PE)	ABCN(PE)	V11
2	ABCN(PE)	(PE)NCBA	V12
3	ABCN(PE)	CBAN(PE)	V13
4	ABCN(PE)	(PE)NABC	V14
5	(PE)NCBA	ABCN(PE)	V21
6	(PE)NCBA	(PE)NCBA	V22
7	(PE)NCBA	CBAN(PE)	V23
8	(PE)NCBA	(PE)NABC	V24
9	CBAN(PE)	ABCN(PE)	V31
10	CBAN(PE)	(PE)NCBA	V32
11	CBAN(PE)	CBAN(PE)	V33
12	CBAN(PE)	(PE)NABC	V34
13	(PE)NABC	ABCN(PE)	V41
14	(PE)NABC	(PE)NCBA	V42
15	(PE)NABC	CBAN(PE)	V43
16	(PE)NABC	(PE)NABC	V44

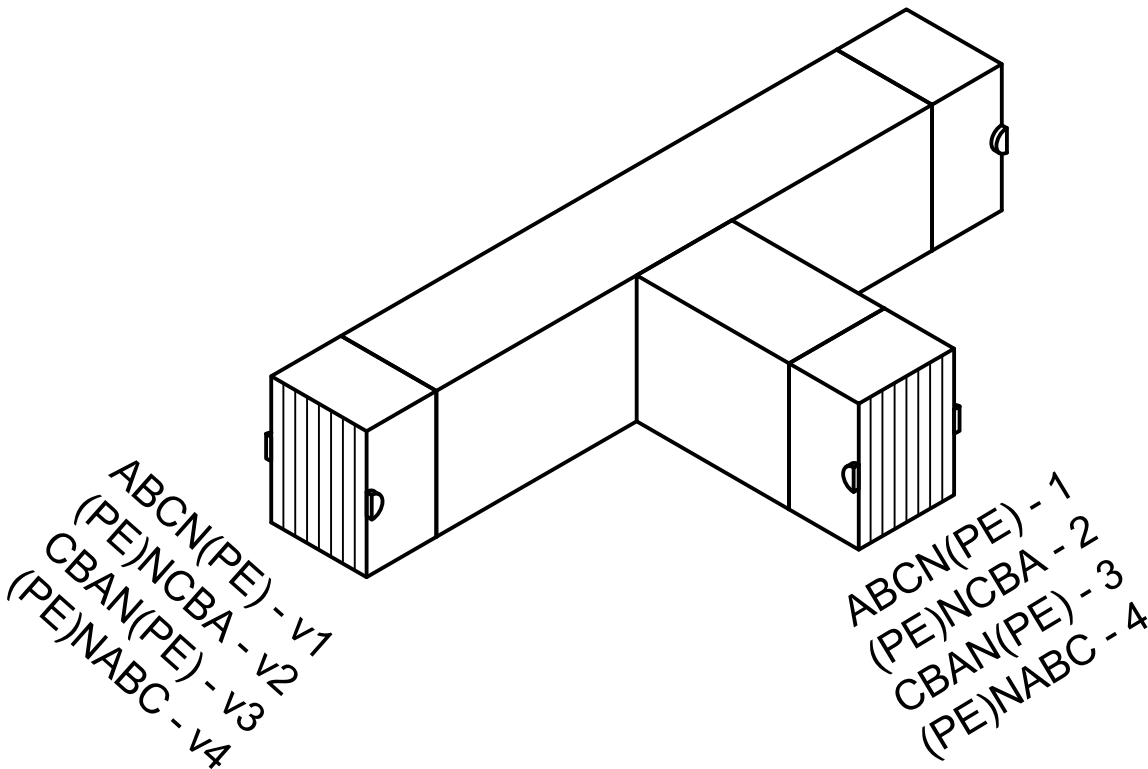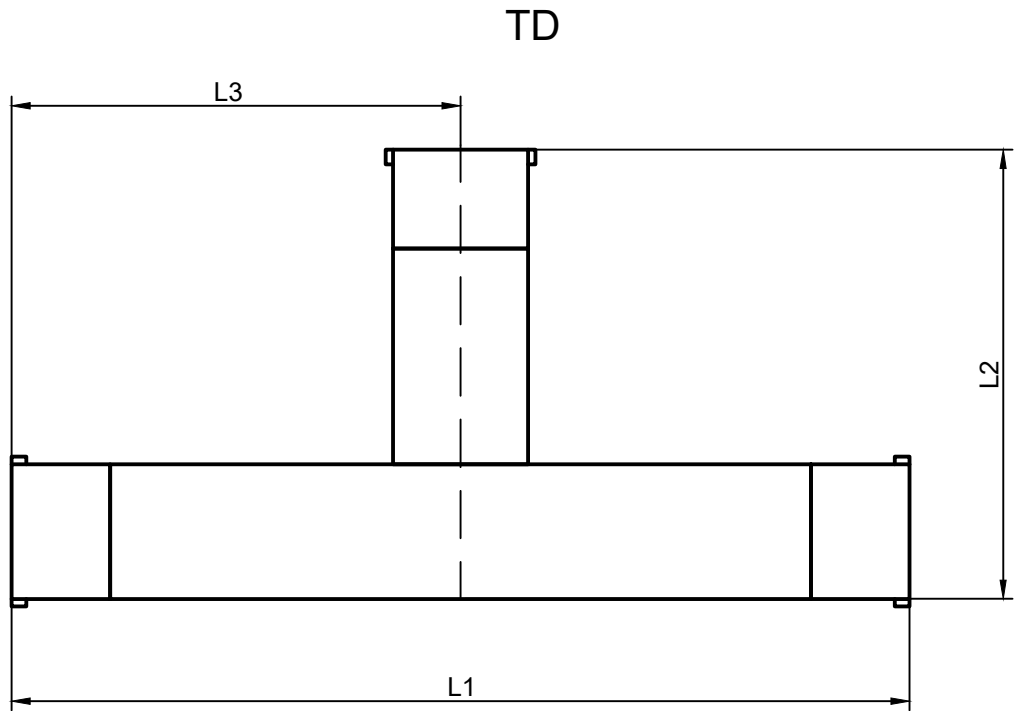

1. Габаритные размеры указываются от оси стыка.

Пример обозначения попок для хранения секций:
13.25.xxx.012.000-Vxx-L1xL2xL3
В случае добавления в секции типа, то наименование
следует принимать как:
13.25.xxx.012.000-Vxx-txx-L1xL2xL3

Разделитель между L - латинская 'x'.

Изм.	Кол.уч	Лист	№ док.	Подп.	Дата	Эскизы секций версия 7			
Разраб.	Елдин Е.В.				10.25	Секции шинопровода	Стадия	Лист	Листов
Проверил	Банников Е.Д.				10.25		Р	6	7
Утвердил	Банников П.В.				10.25				

Technical drawing of a mechanical part, likely a bracket or support. The drawing shows a cross-section with a central vertical shaft and a horizontal base. The dimensions are labeled as follows:

- $L1$: The height of the central vertical shaft.
- $L2^*$: The total height of the part, including the base.
- 210 : The width of the base.

Technical drawing of a mechanical part, likely a bracket or support. The drawing shows a side view with the following dimensions:



- L1**: Vertical dimension of the main body.
- L2**: Horizontal dimension of the main body.
- L3**: Horizontal dimension of the main body.
- 210**: Vertical dimension of the base.

The drawing includes a circular feature on the right side of the main body and a series of small circles (possibly holes or mounting points) on the base.

Technical drawing of a mechanical part, likely a bracket or support. The drawing shows a side view with the following dimensions:

- L1**: Vertical dimension of the main body.
- L2***: Total vertical dimension from the base to the top of the main body.
- L3**: Horizontal dimension of the main body.
- 210**: Vertical dimension of the base.

ABCN(PE) - v1
(PE)NCBA - v2
CBAN(PE) - v3
(PE)NABC - v4

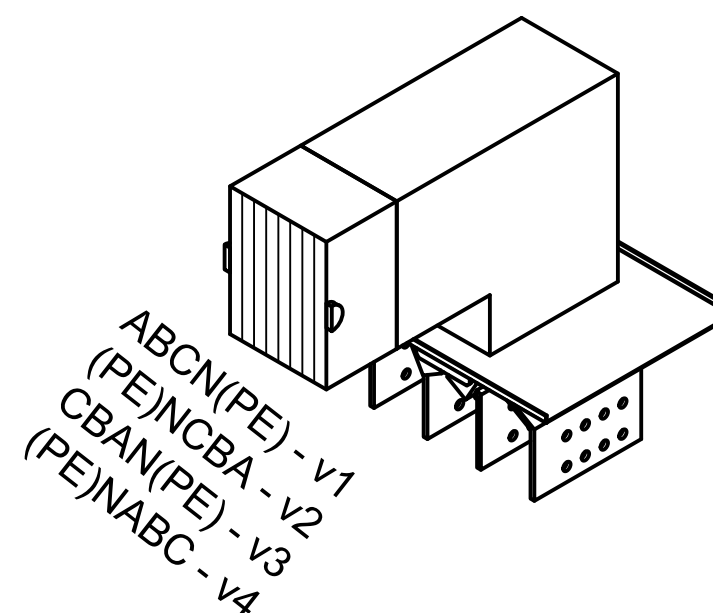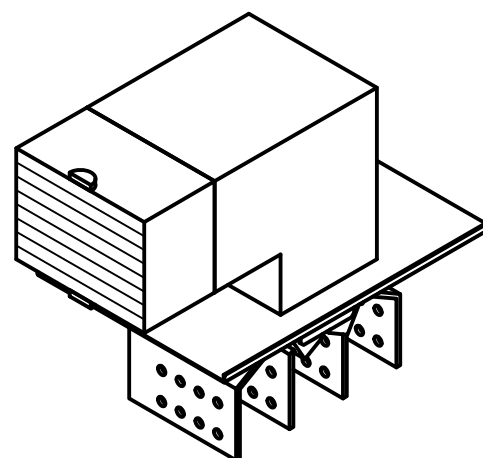

- Пример обозначения попок для хранения секций:
13.25.xxx.012.000-Vxx-L1xL2xL3
- В случае добавления в секции типа, то наименование следует принимать как:
13.25.xxx.012.000-Vxx-txx-L1xL2xL3

						Эскизы секций версия 7			
Изм.	Кол.уч	Лист	№ док.	Подп.	Дата	Секции шинопровода	Стадия	Лист	Листов
Разраб.		Елдин Е.В.			10.25		Р	7	7
Проверил		Банников Е.Д.			10.25				
Утвердил		Банников П.В.			10.25				